



SUMAN GANGOLLI

B. Tech in Civil Engineering
Masters in Civil CAD

Designing a better world in style.



: 8095759406





: sumanpoojary25@gmail.com



TABLE OF CONTENTS

- Concept Drawing
- Working Drawing
- Elevation Drawing
- Section Drawing
- Staircase Drawing
- Lintel Drawing
- Electrical Drawing
- Door - Window Drawing
- Plumbing Drawing
- Building Pipeline Drawing
- Furniture Layout
- Floor Estimation
- Grill Designs
- Tile Layout Design
- General Toilet Layout
- General Electrical Layout
- Interiors
- 3D Elevations
- 3D Floor Plans
- 3D Presentation



CONCEPT DRAWING

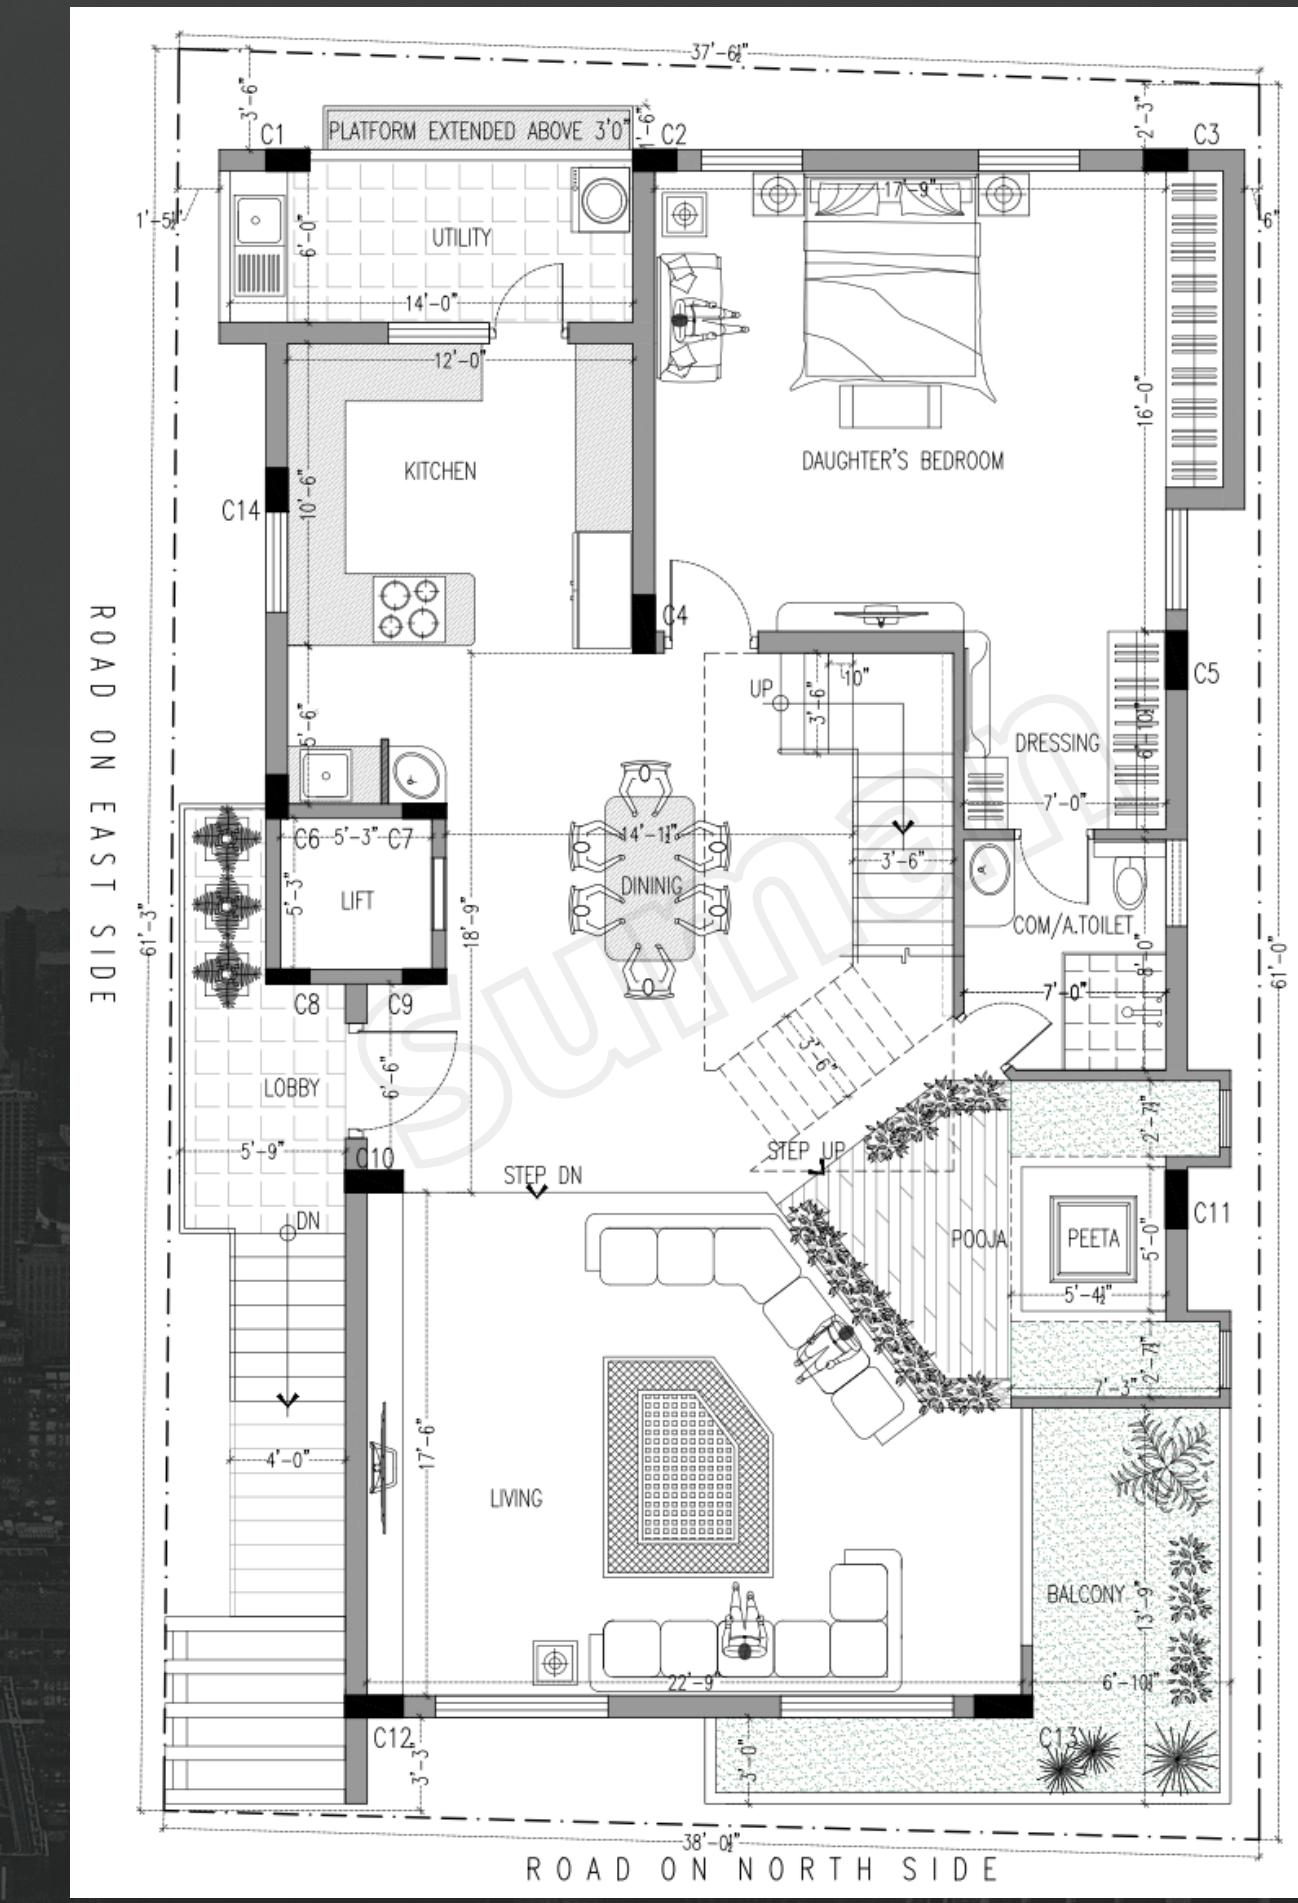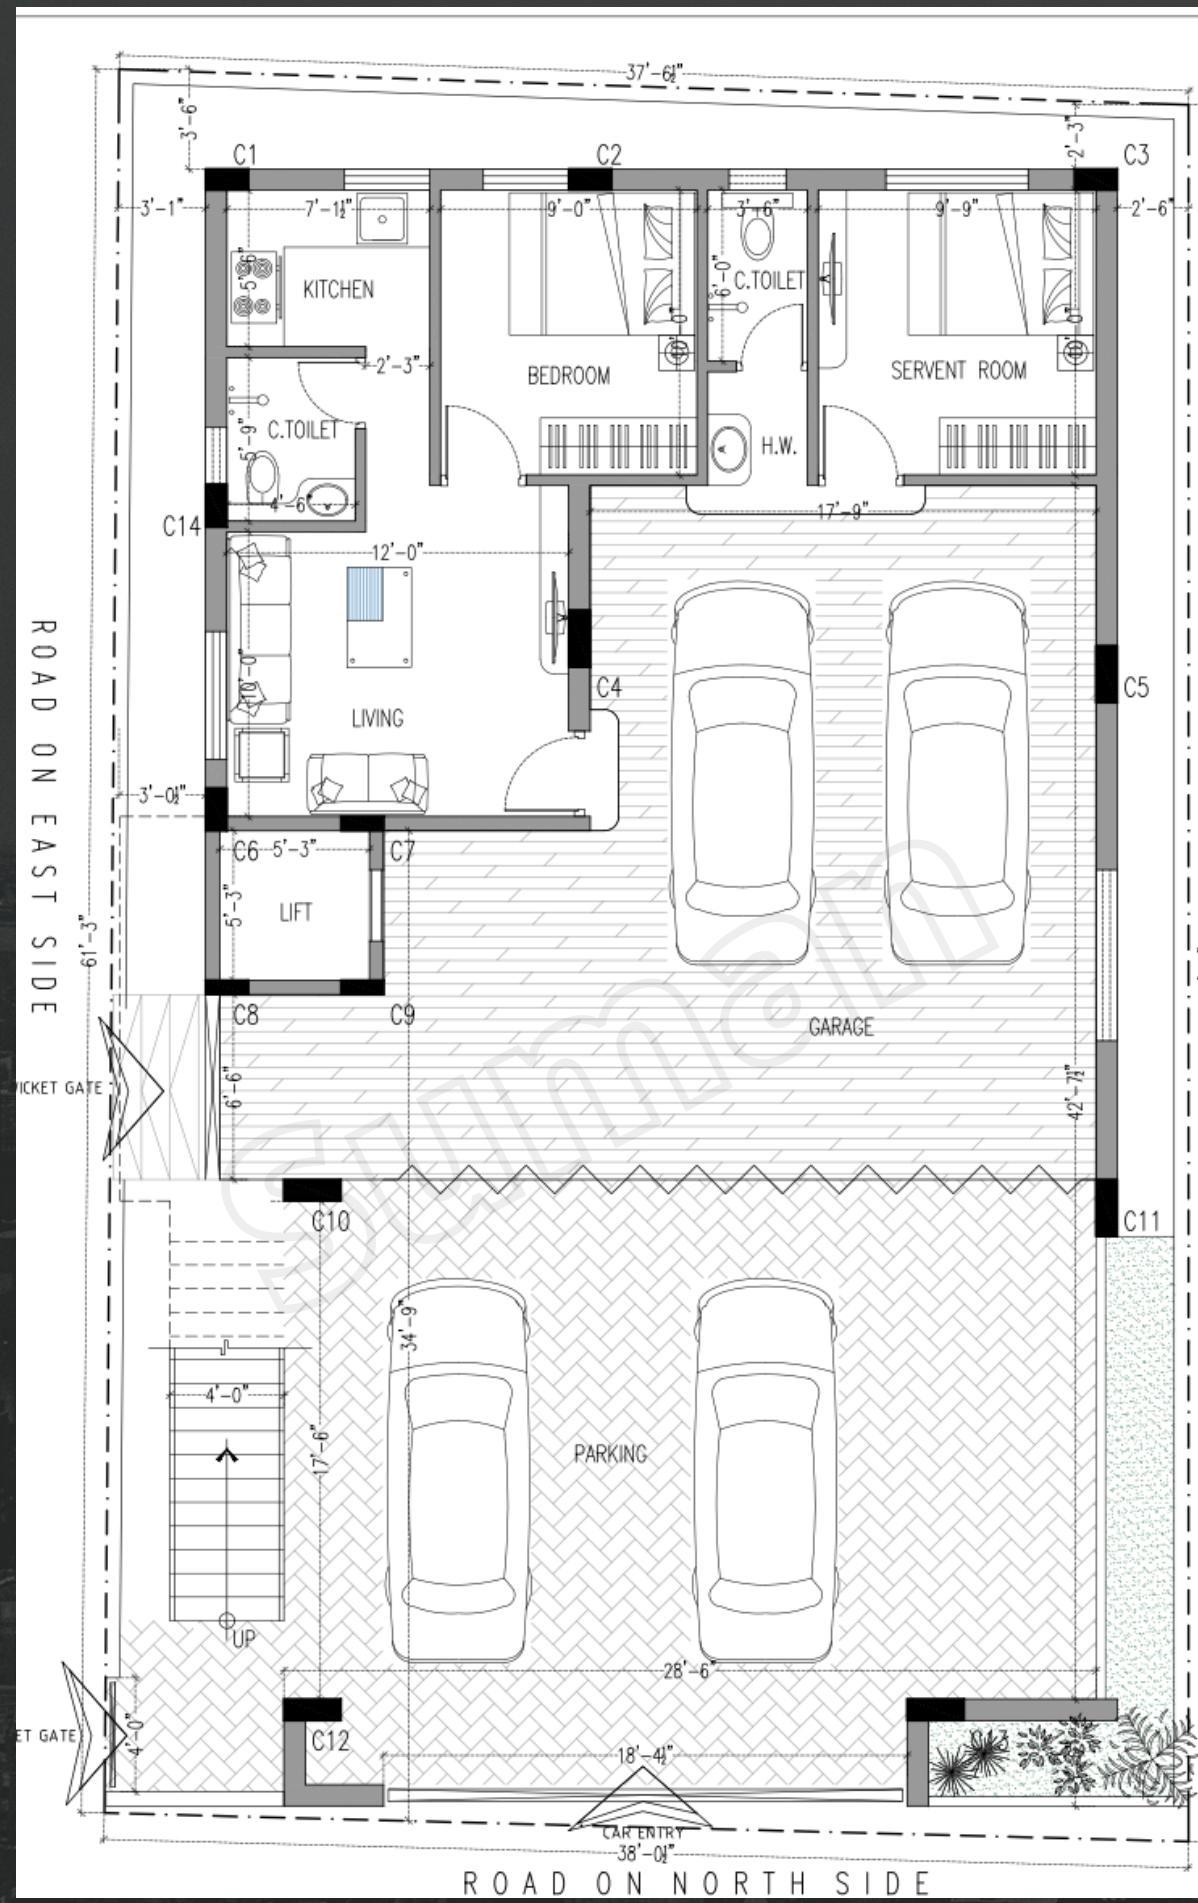




WORKING DRAWING

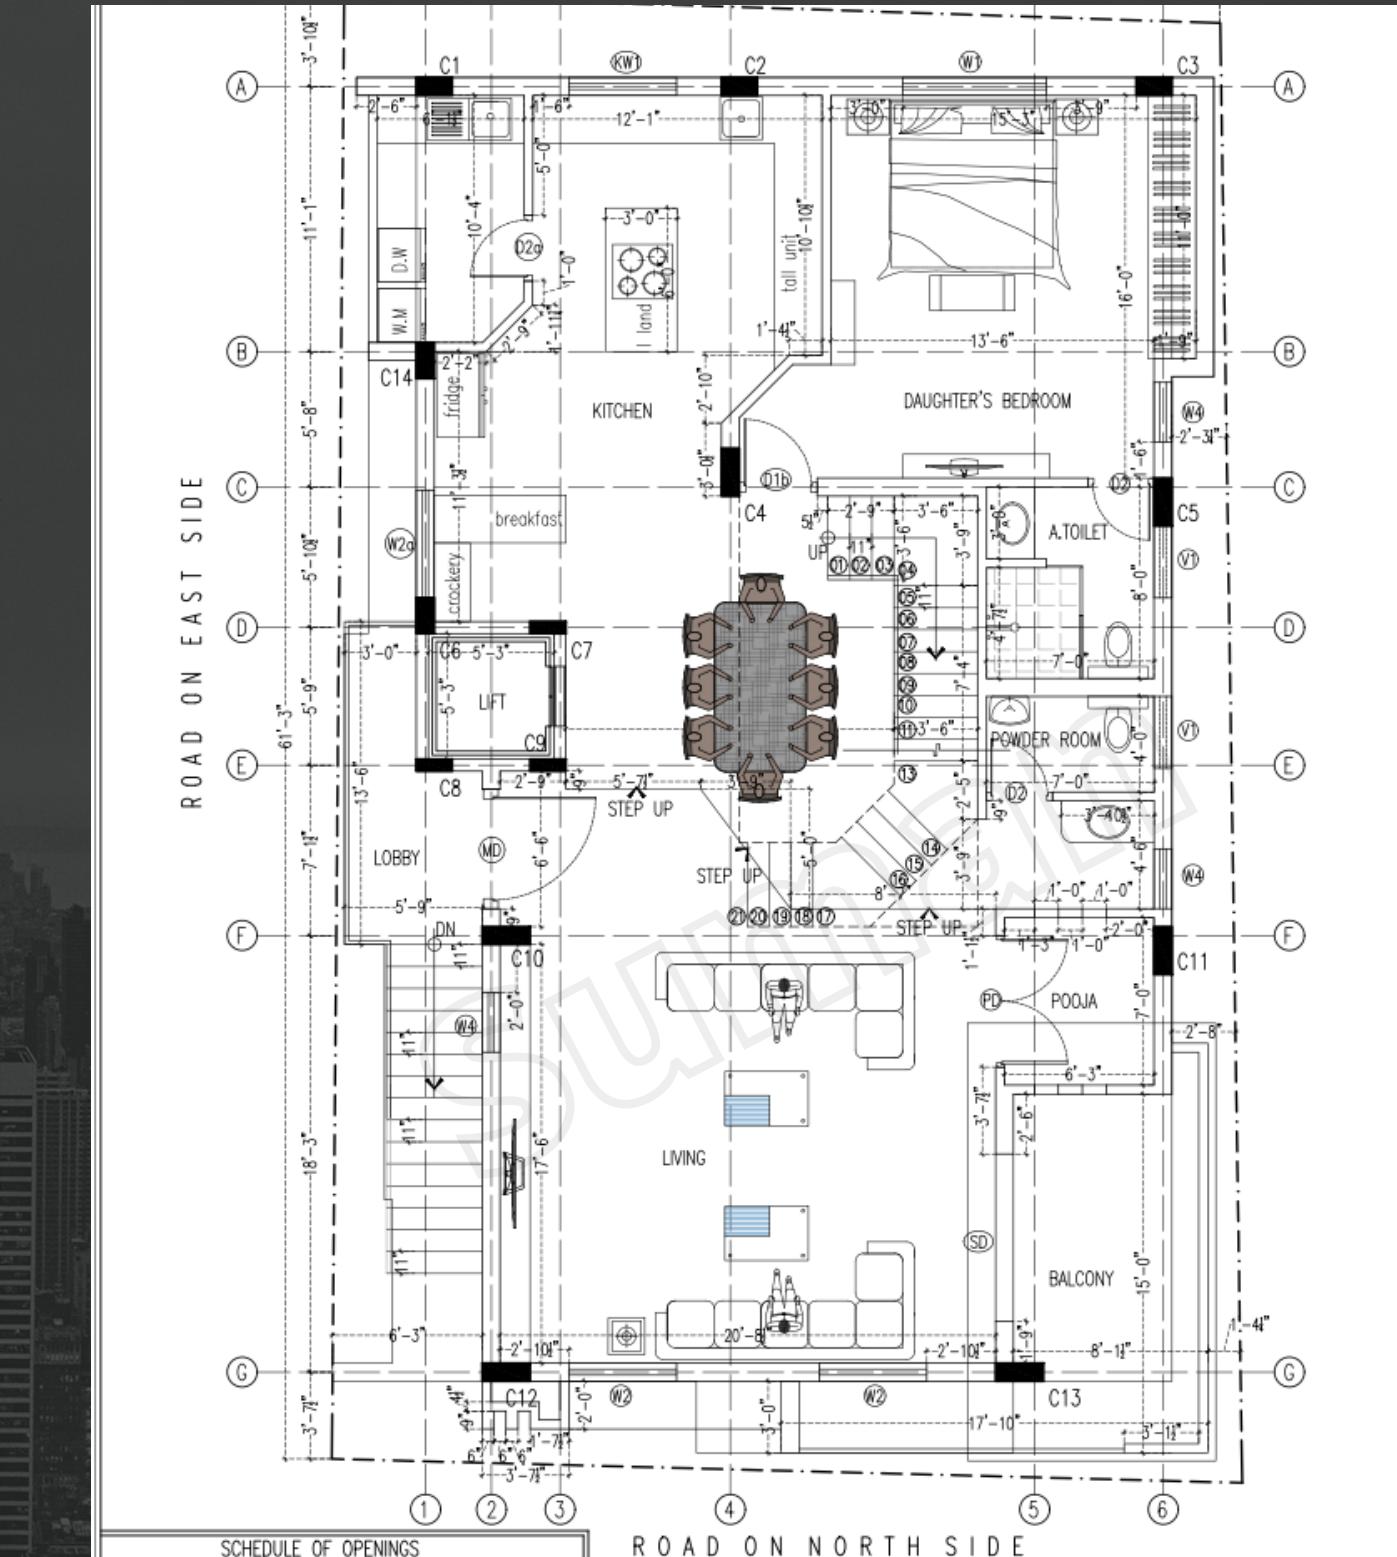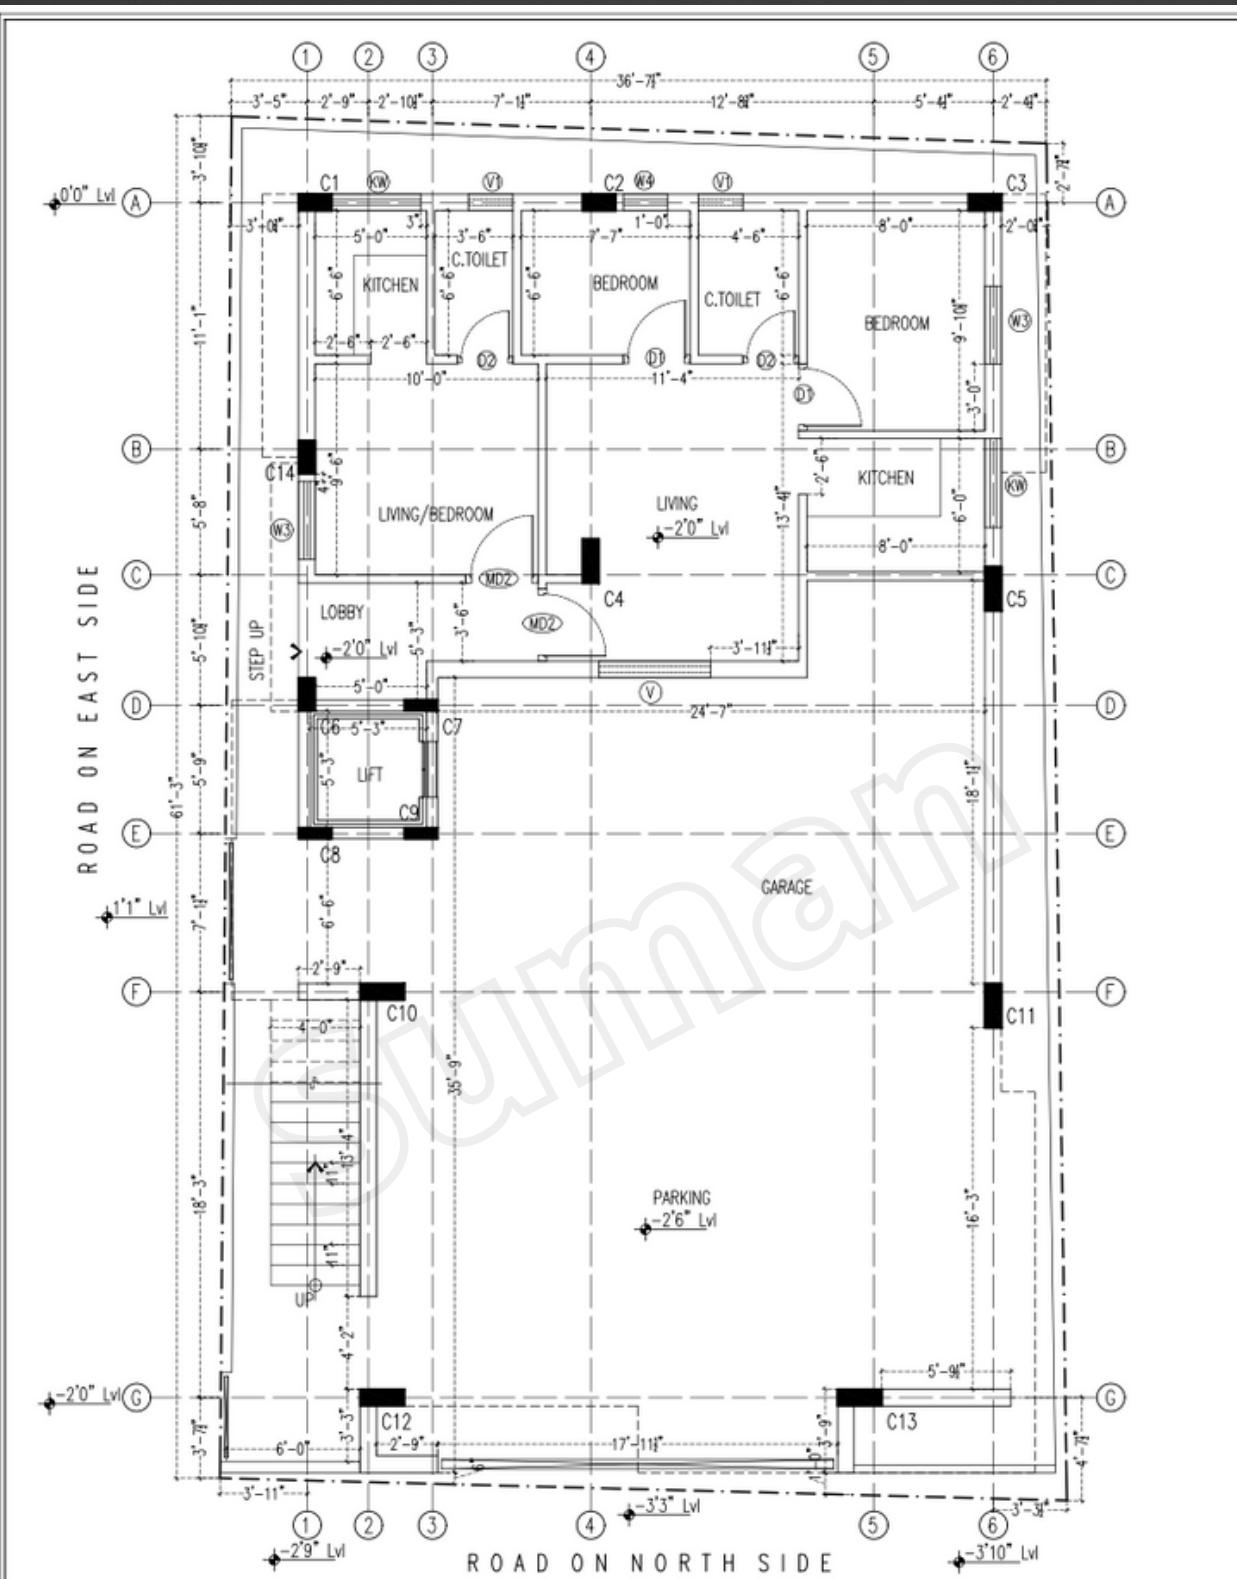



ELEVATION DRAWING

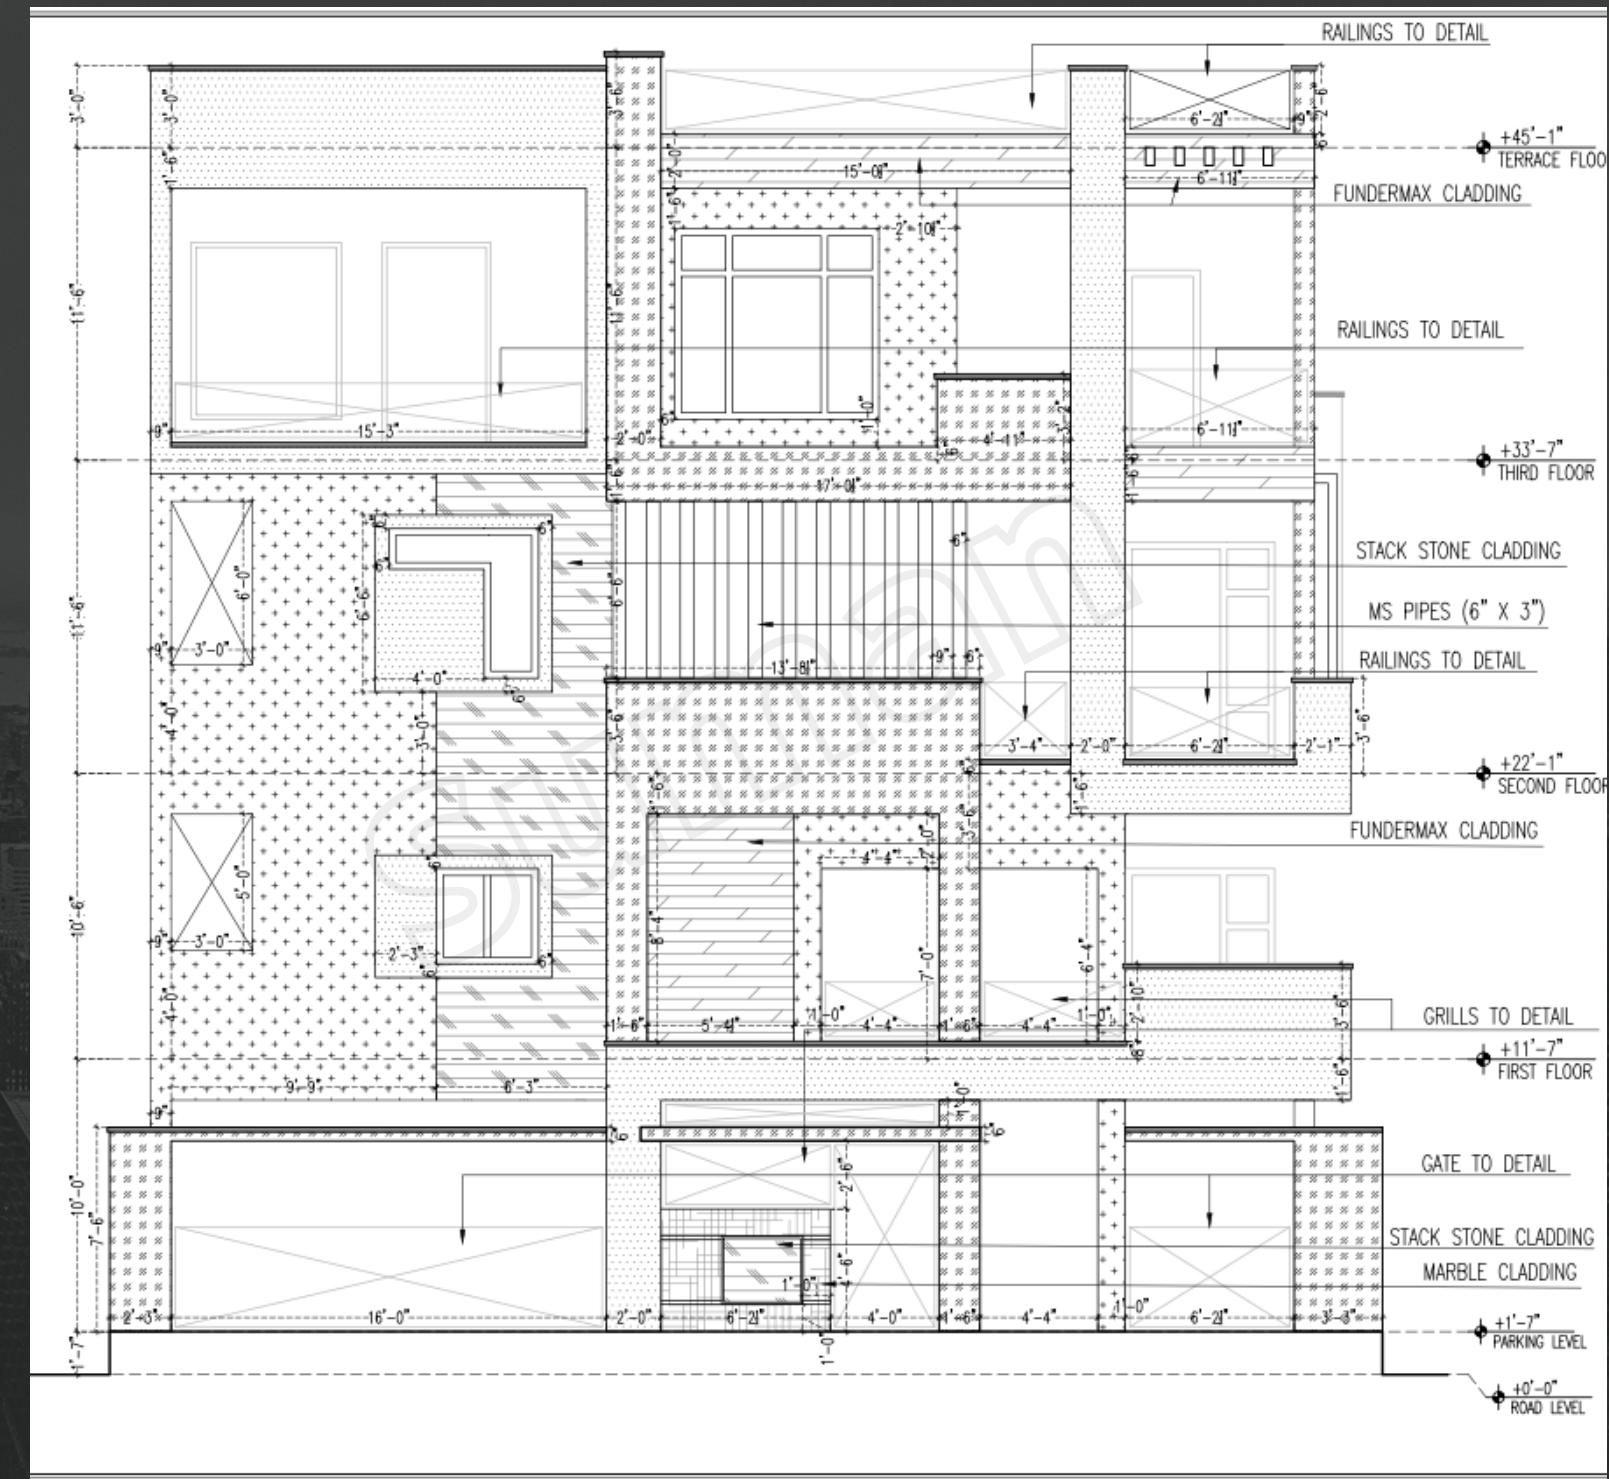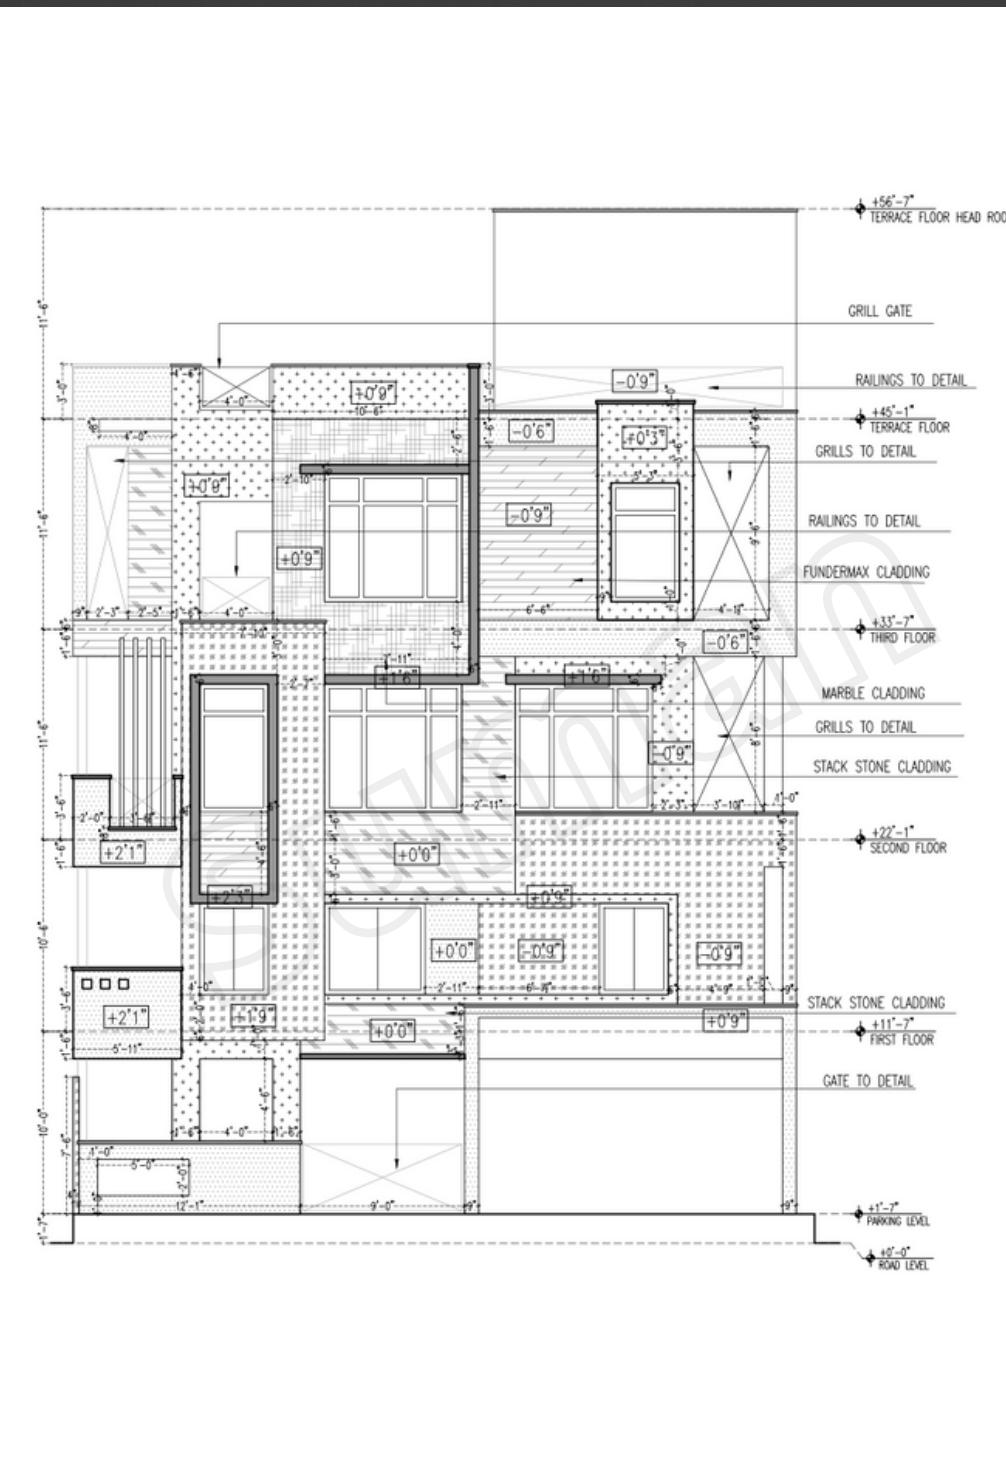



SECTION DRAWING

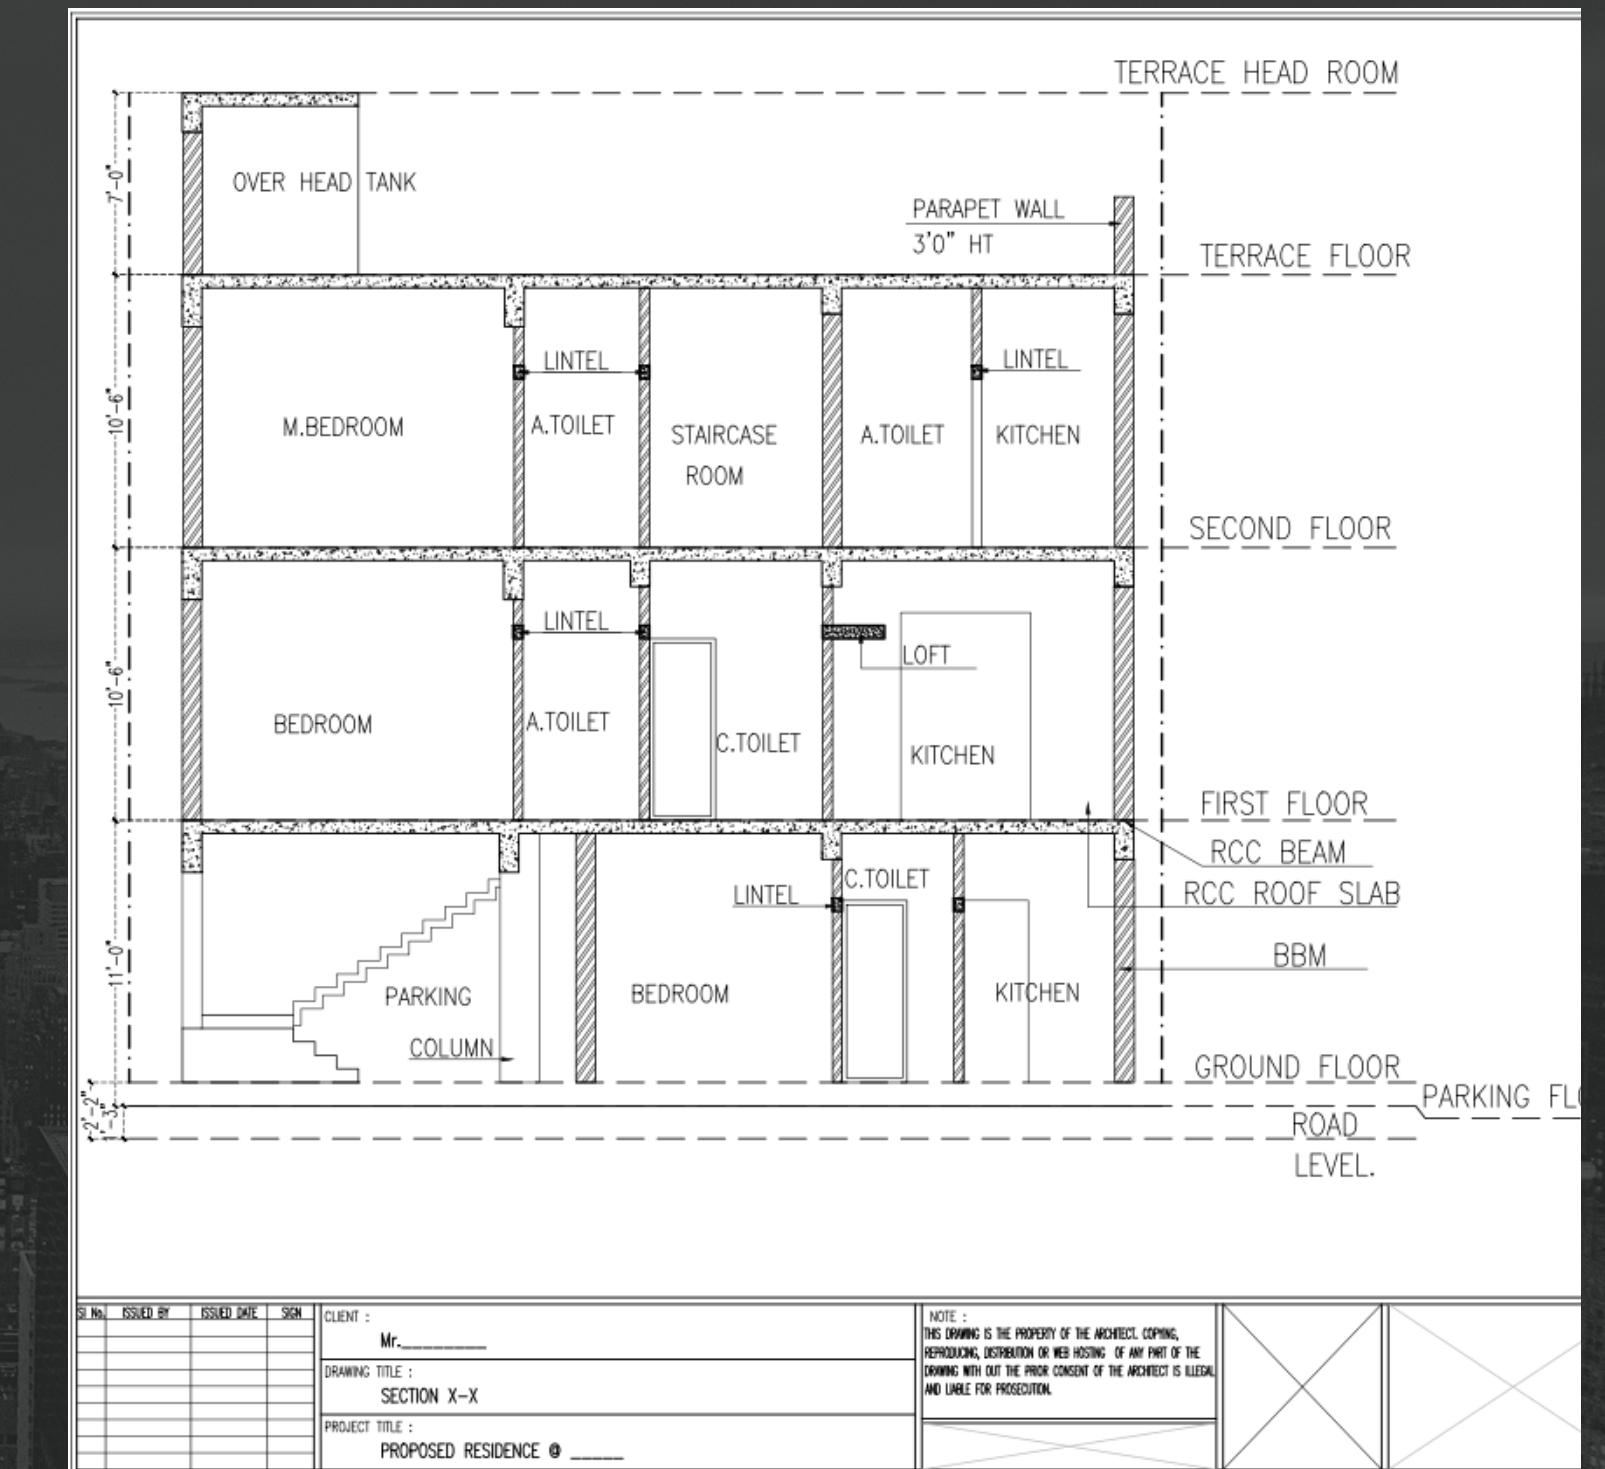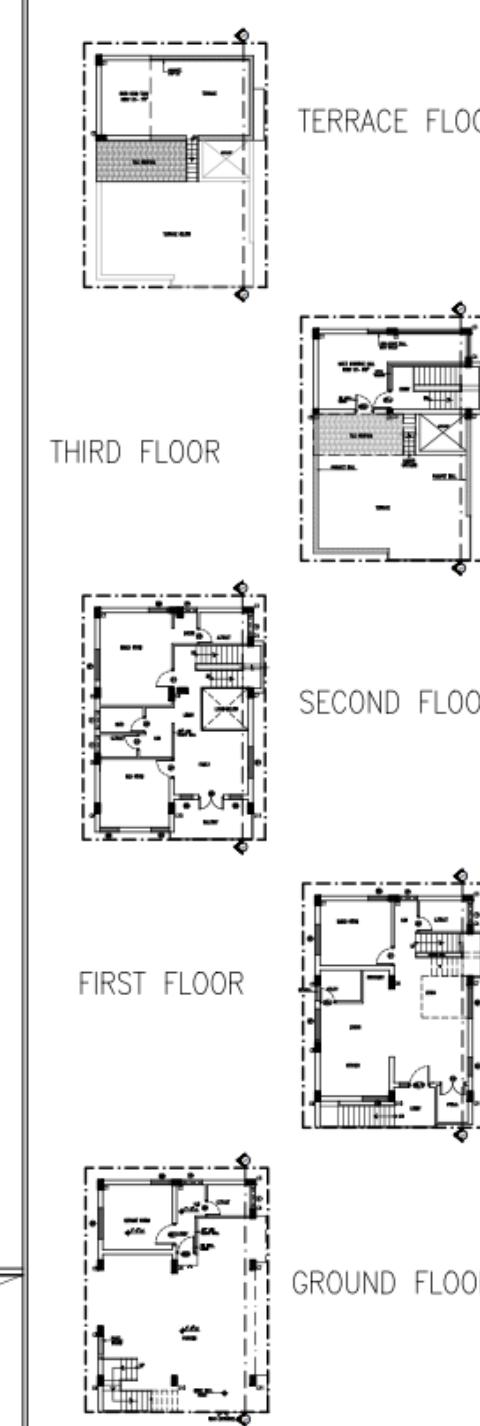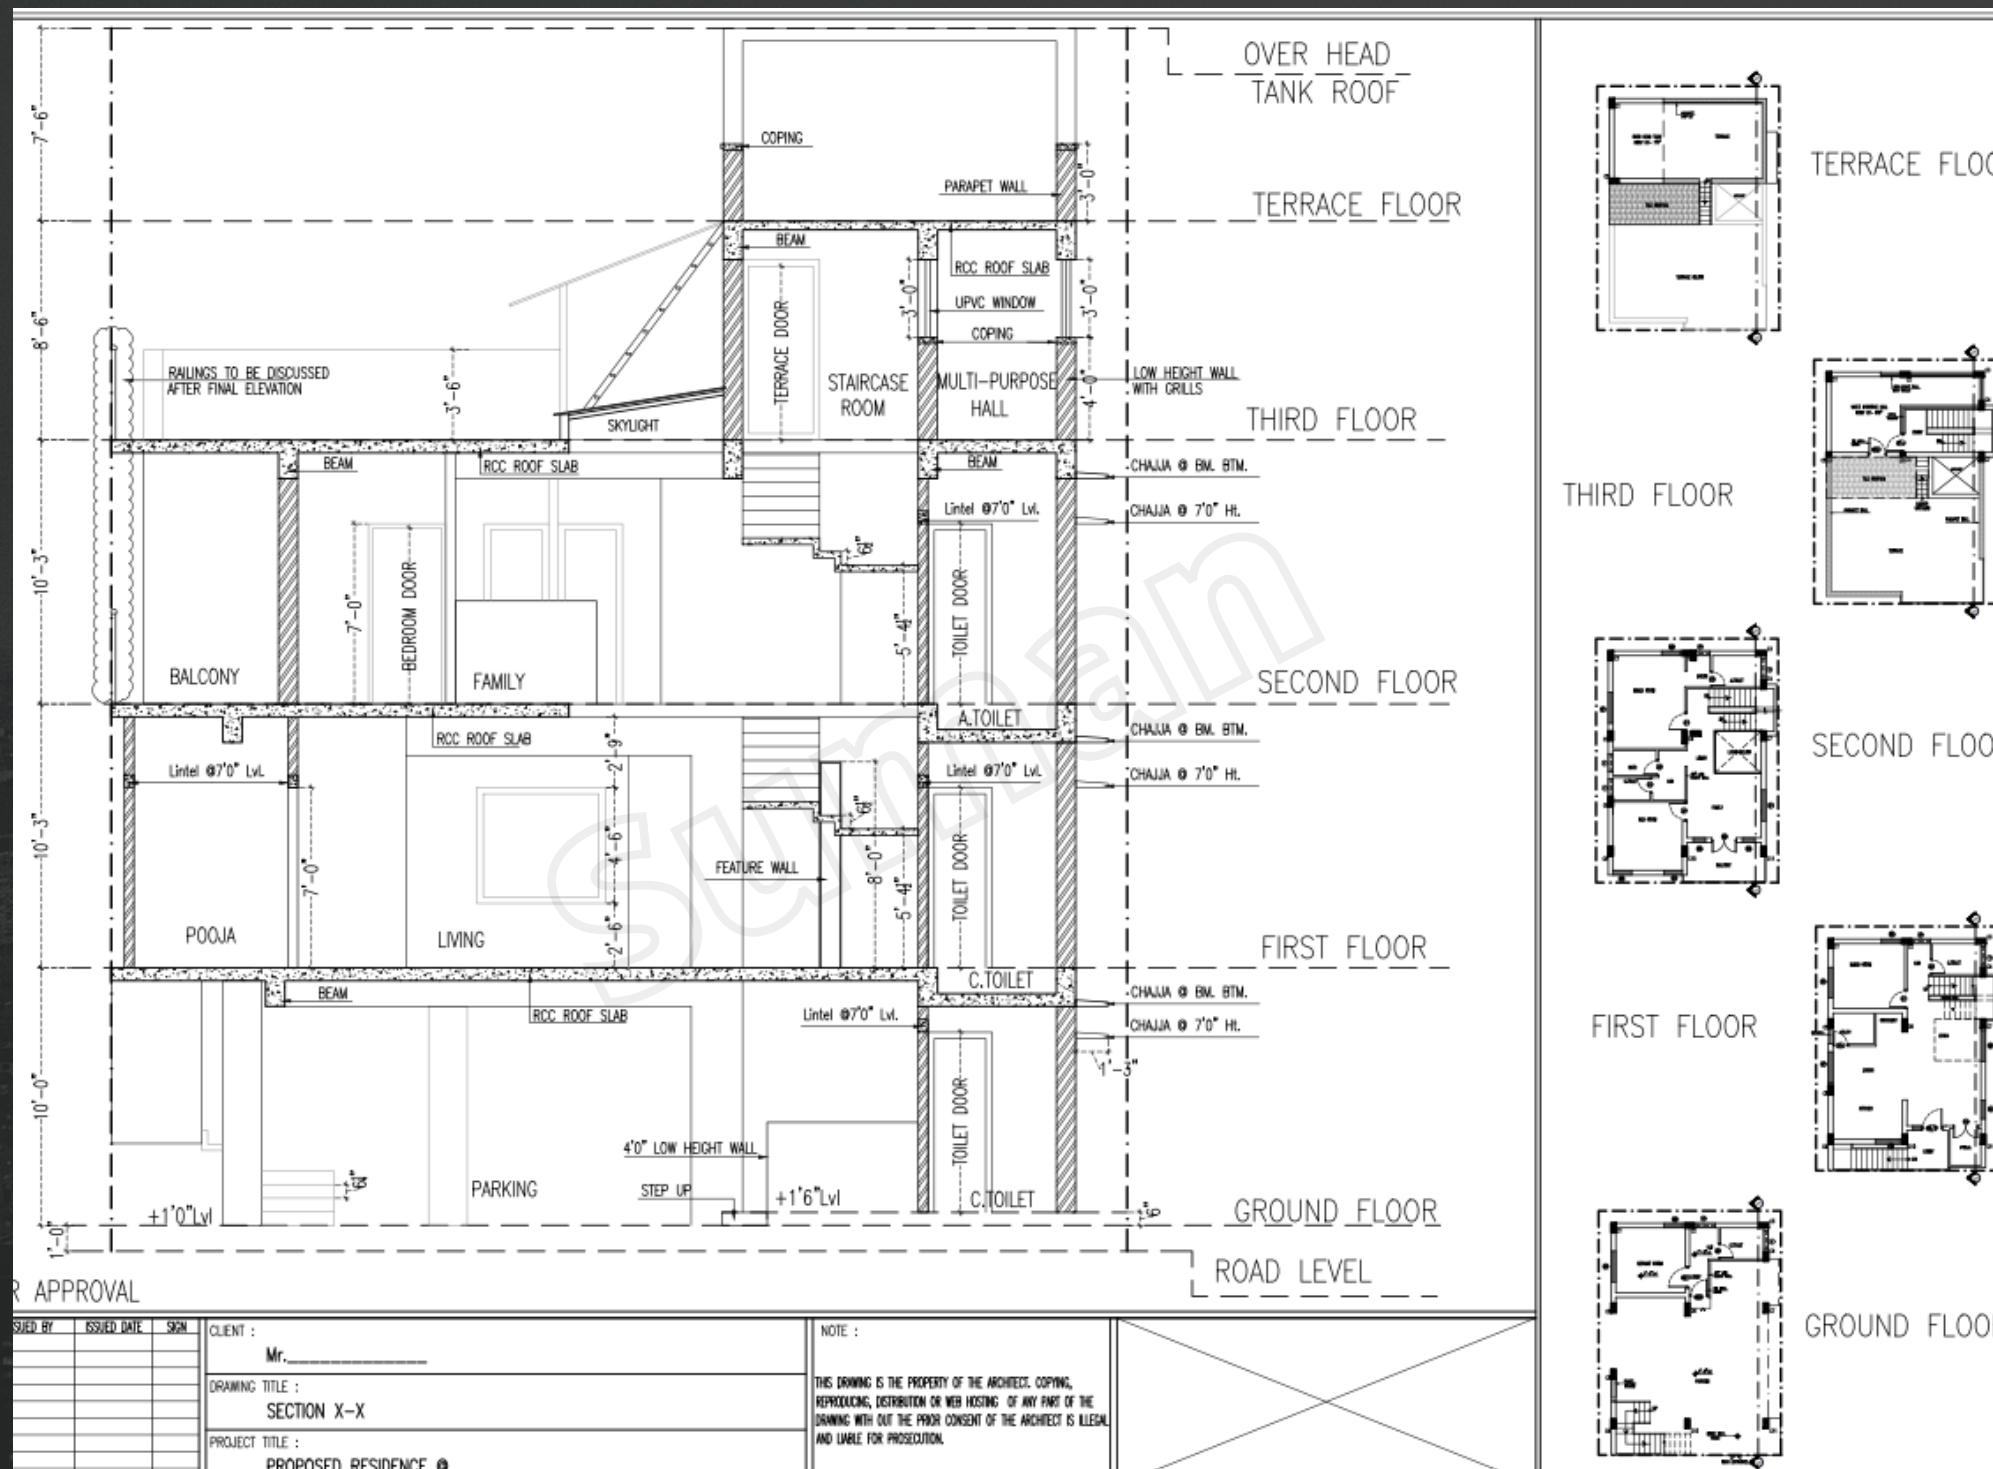



STAIRCASE DRAWING

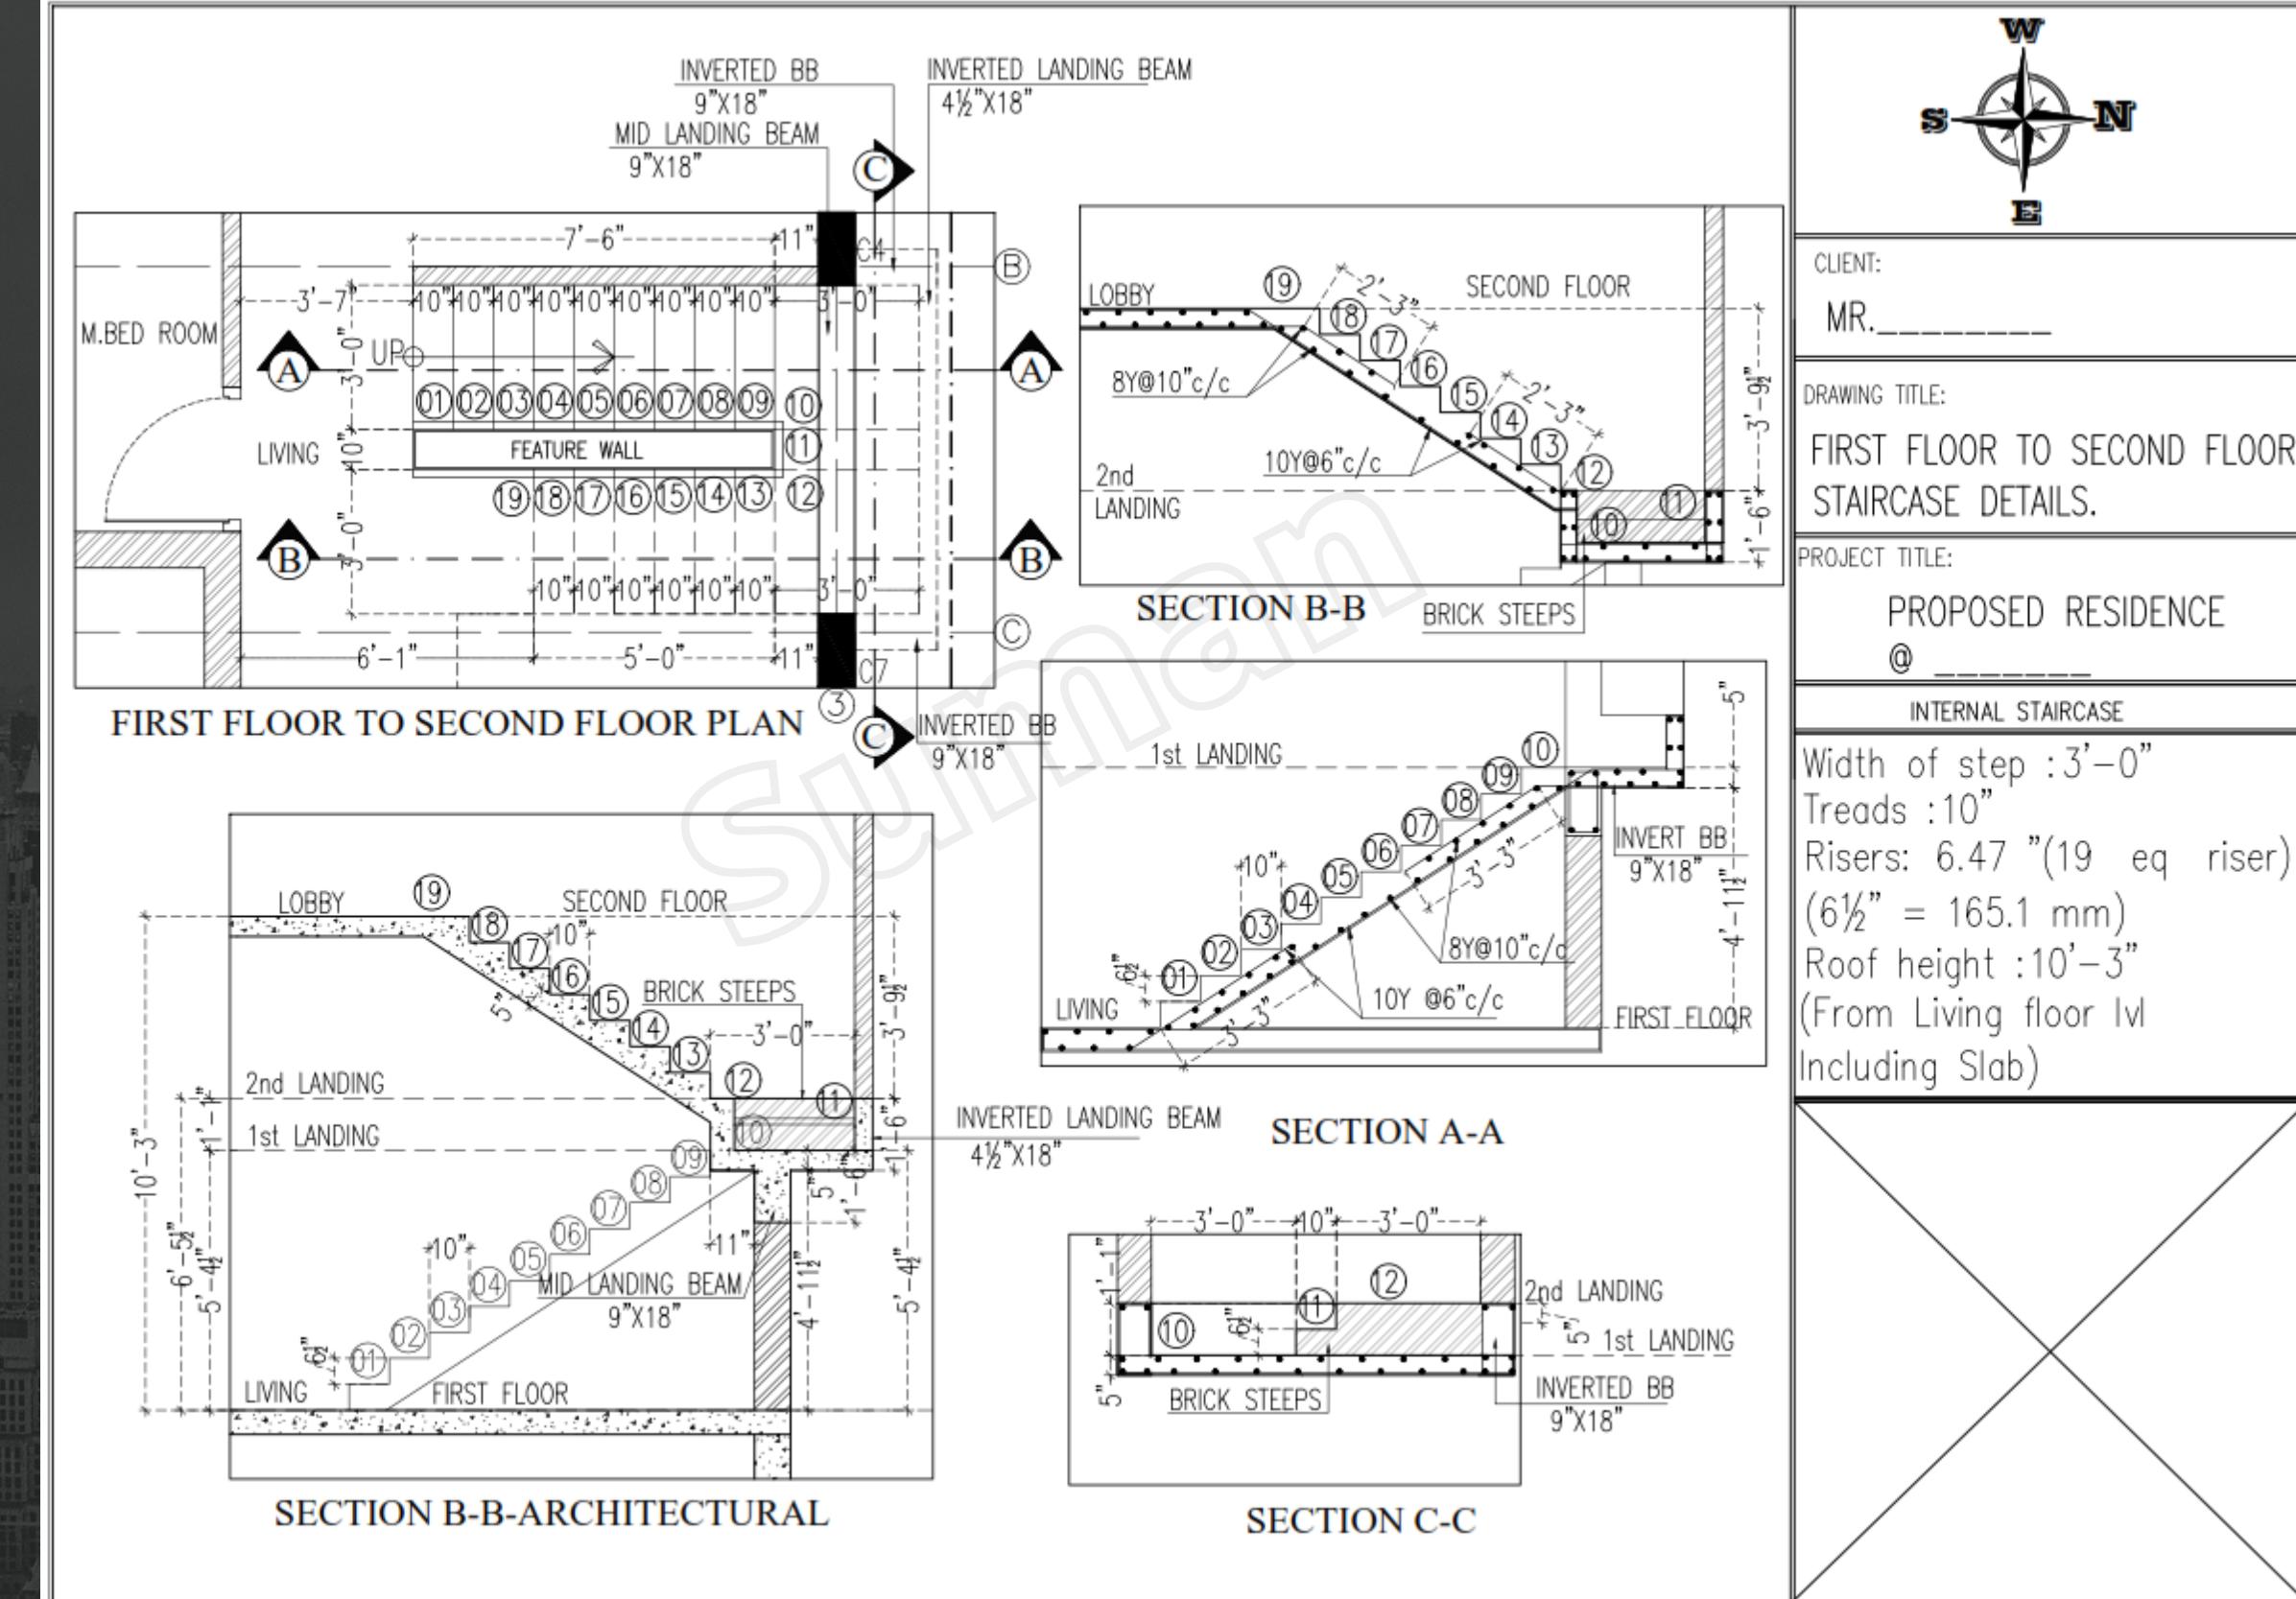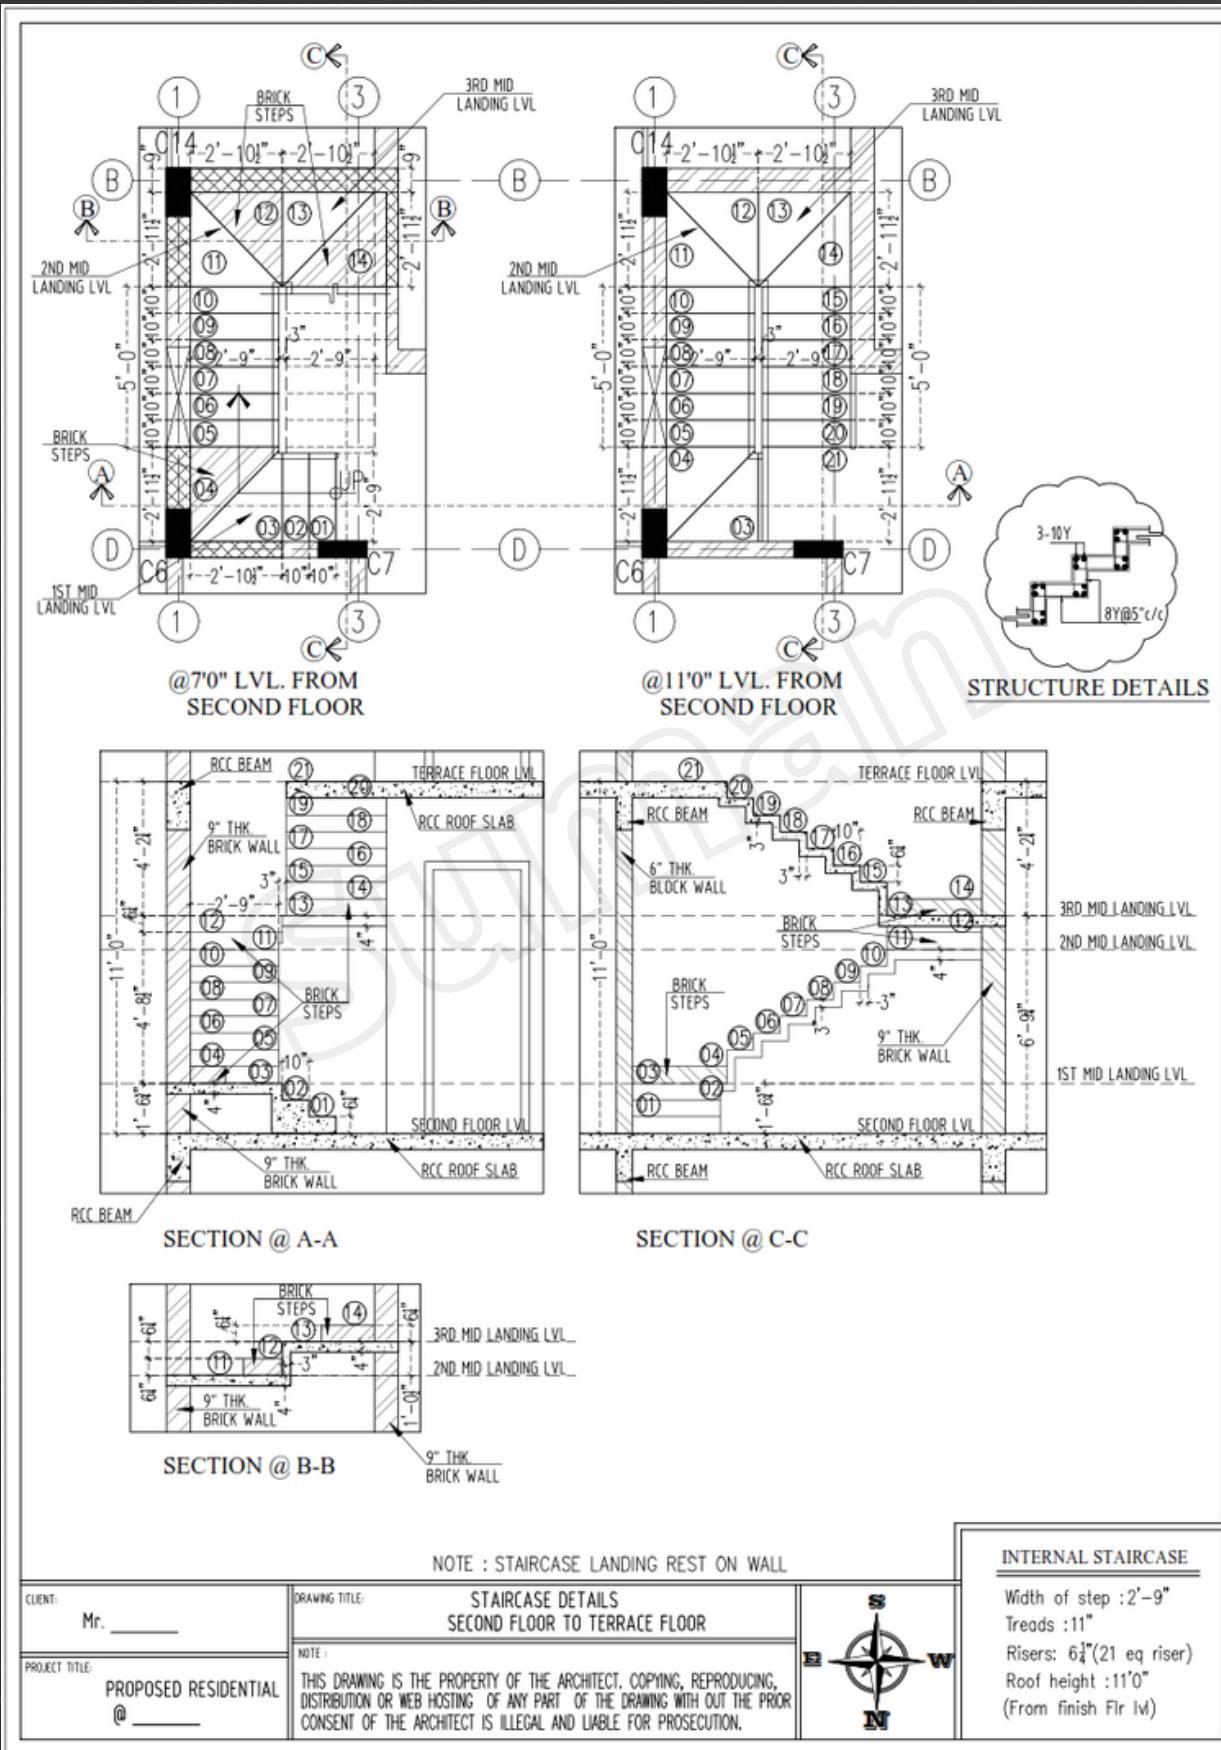



LINTEL DRAWING

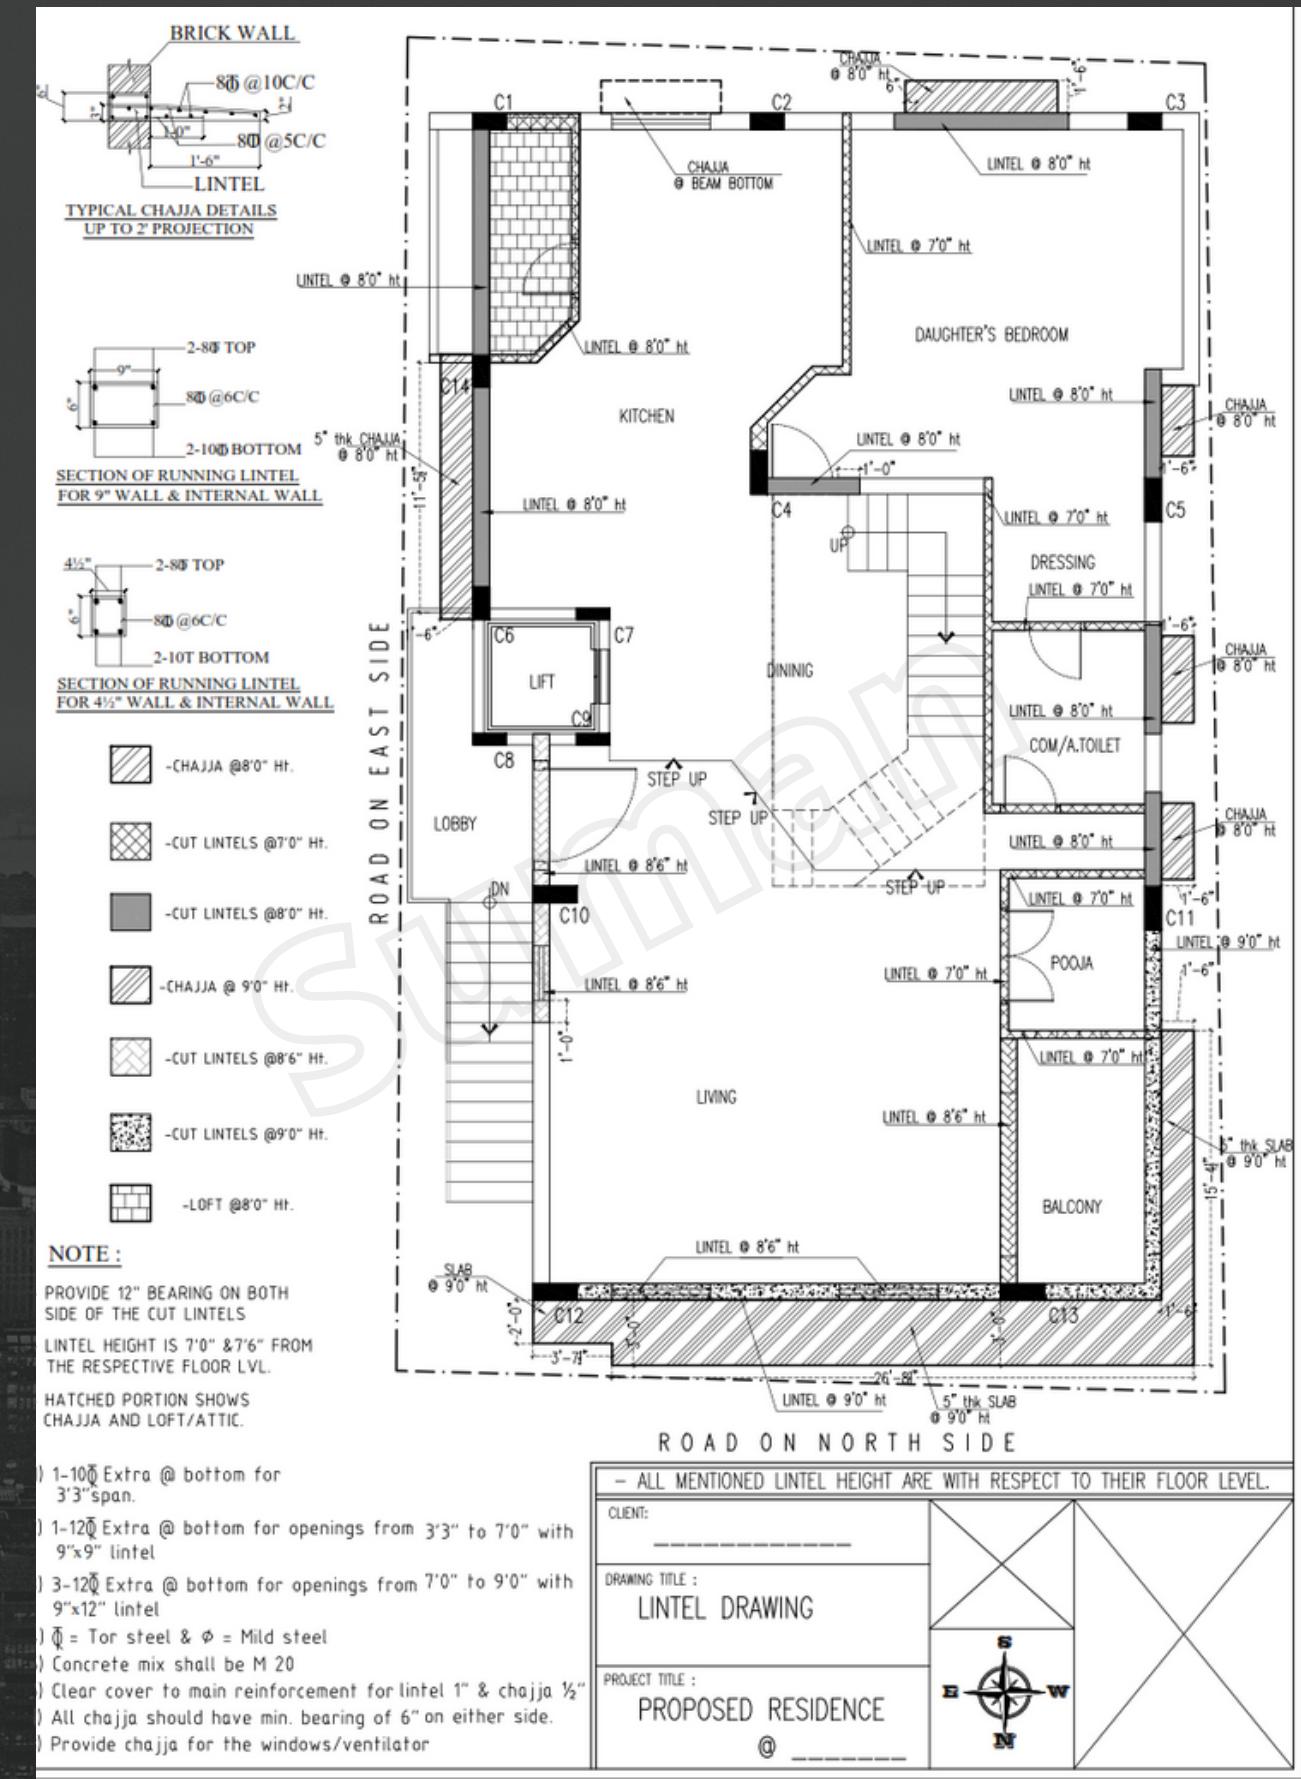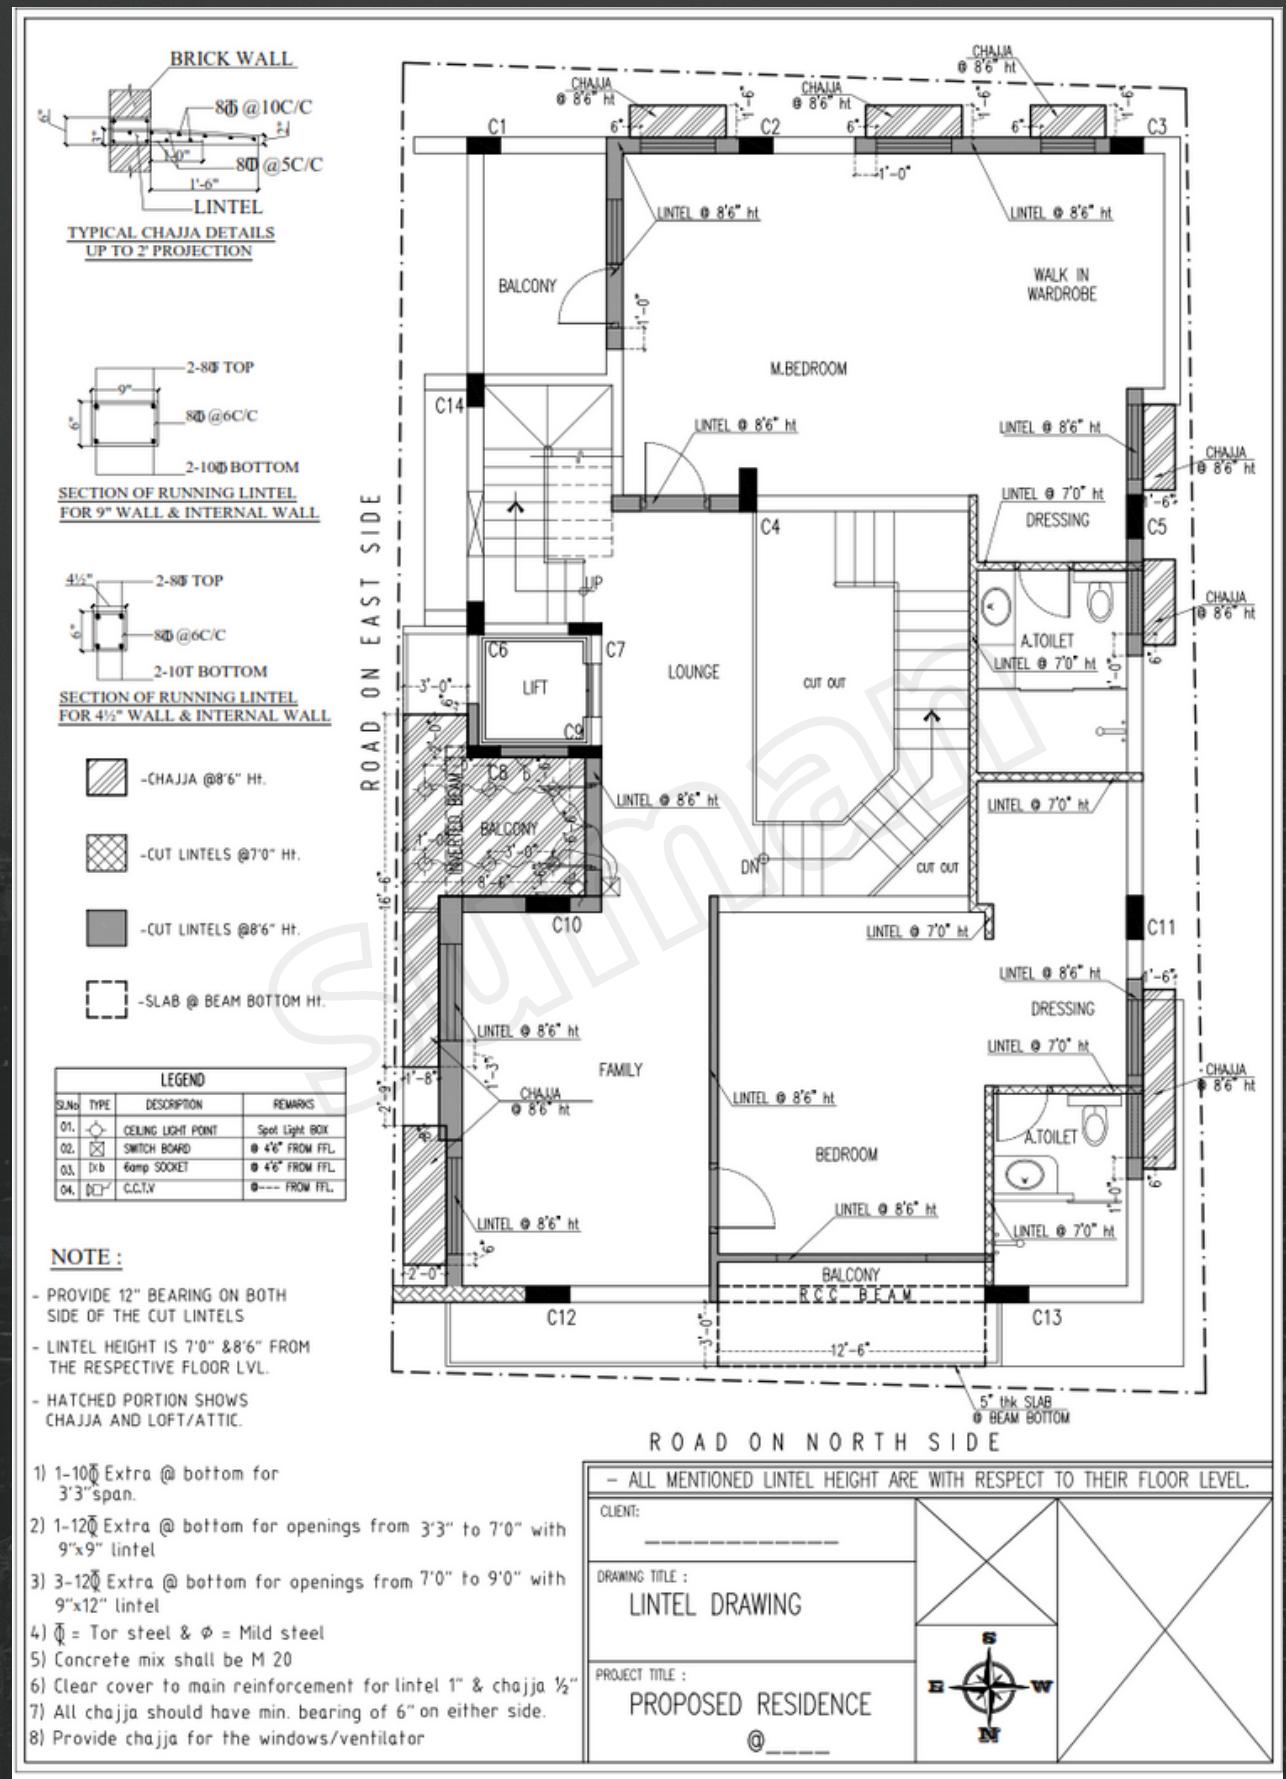

ELECTRICAL DRAWING

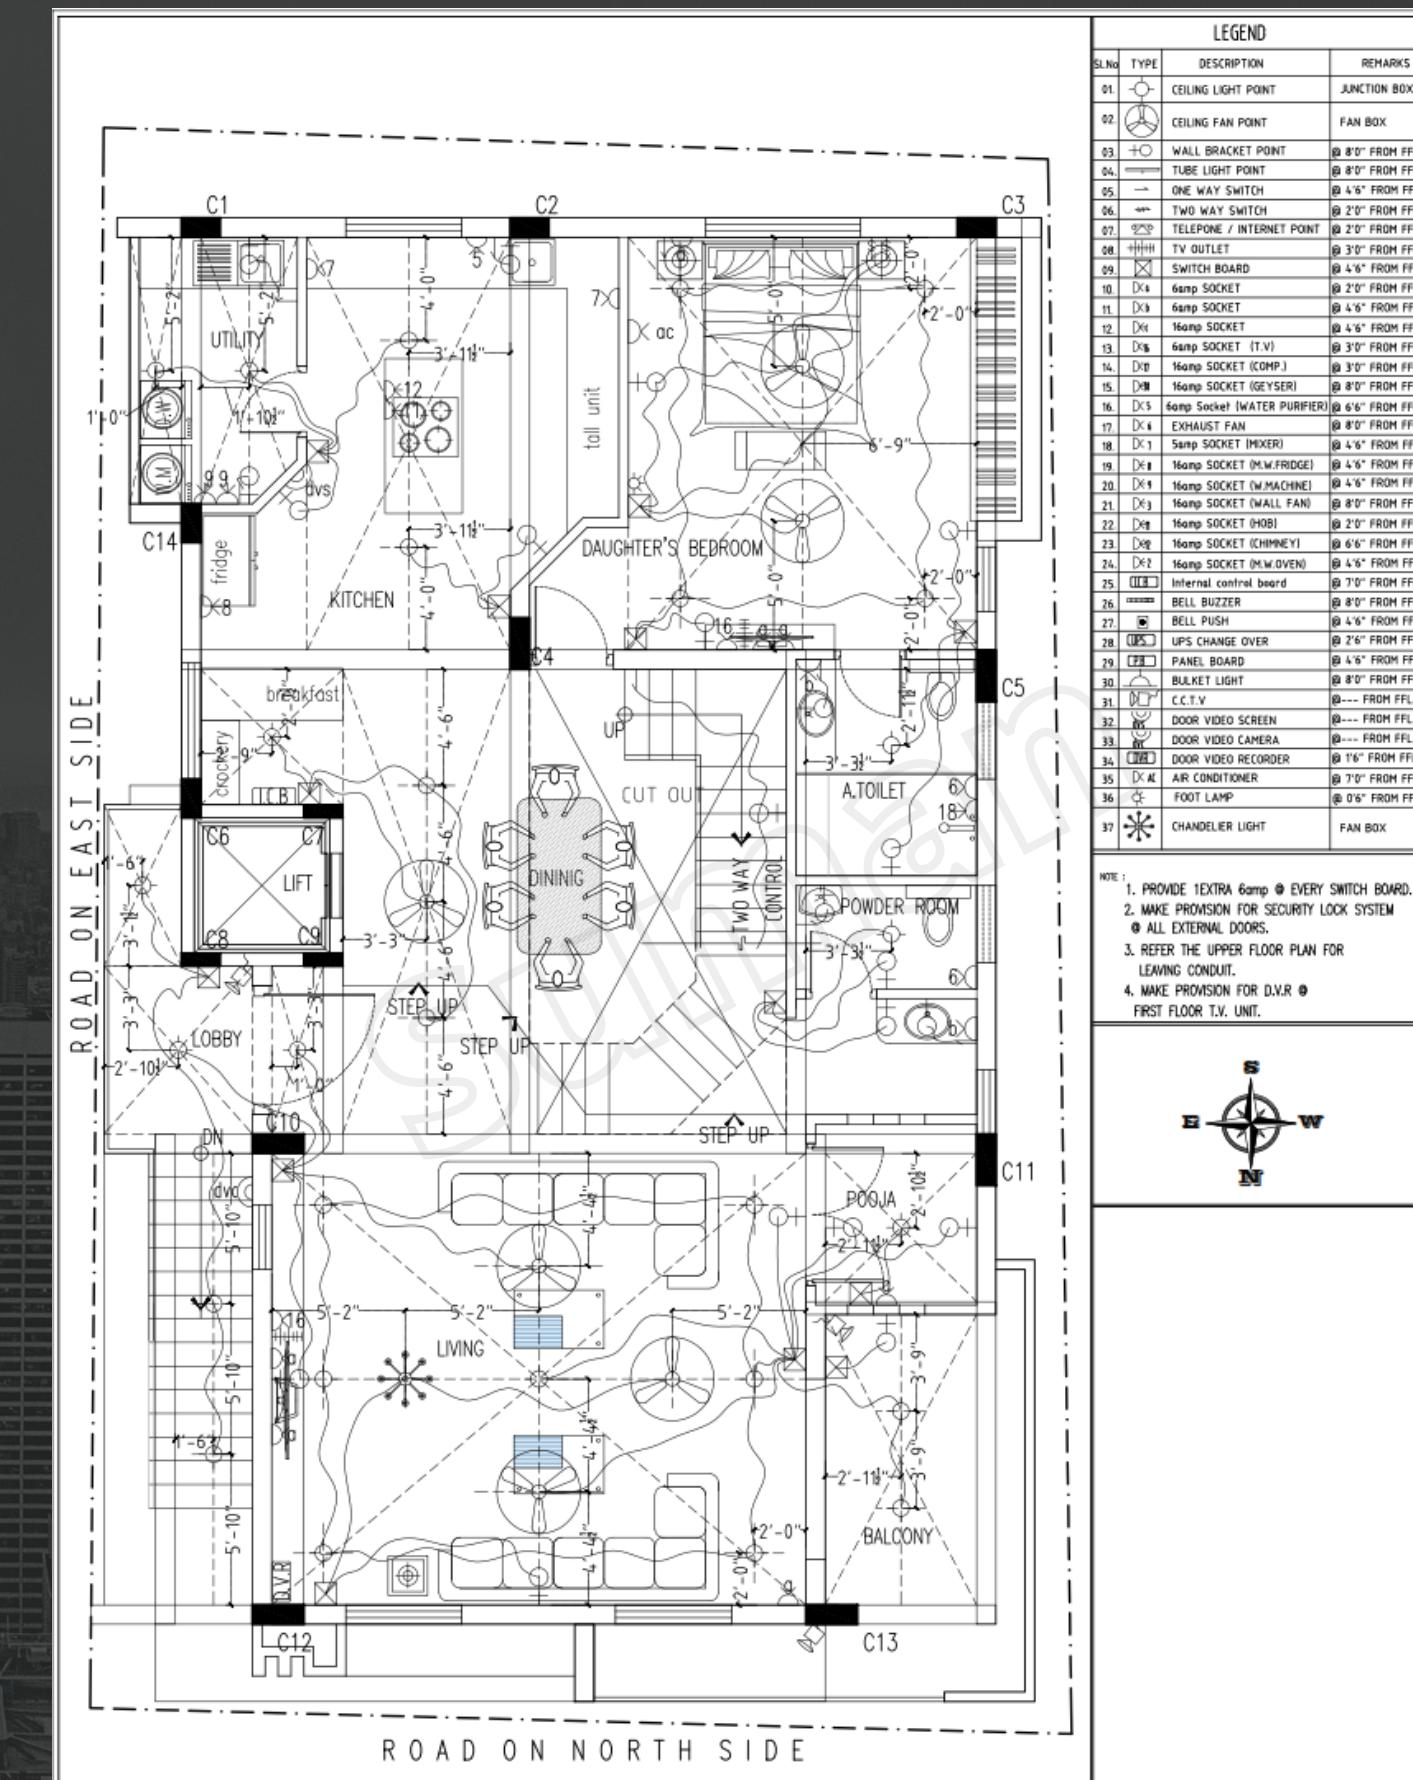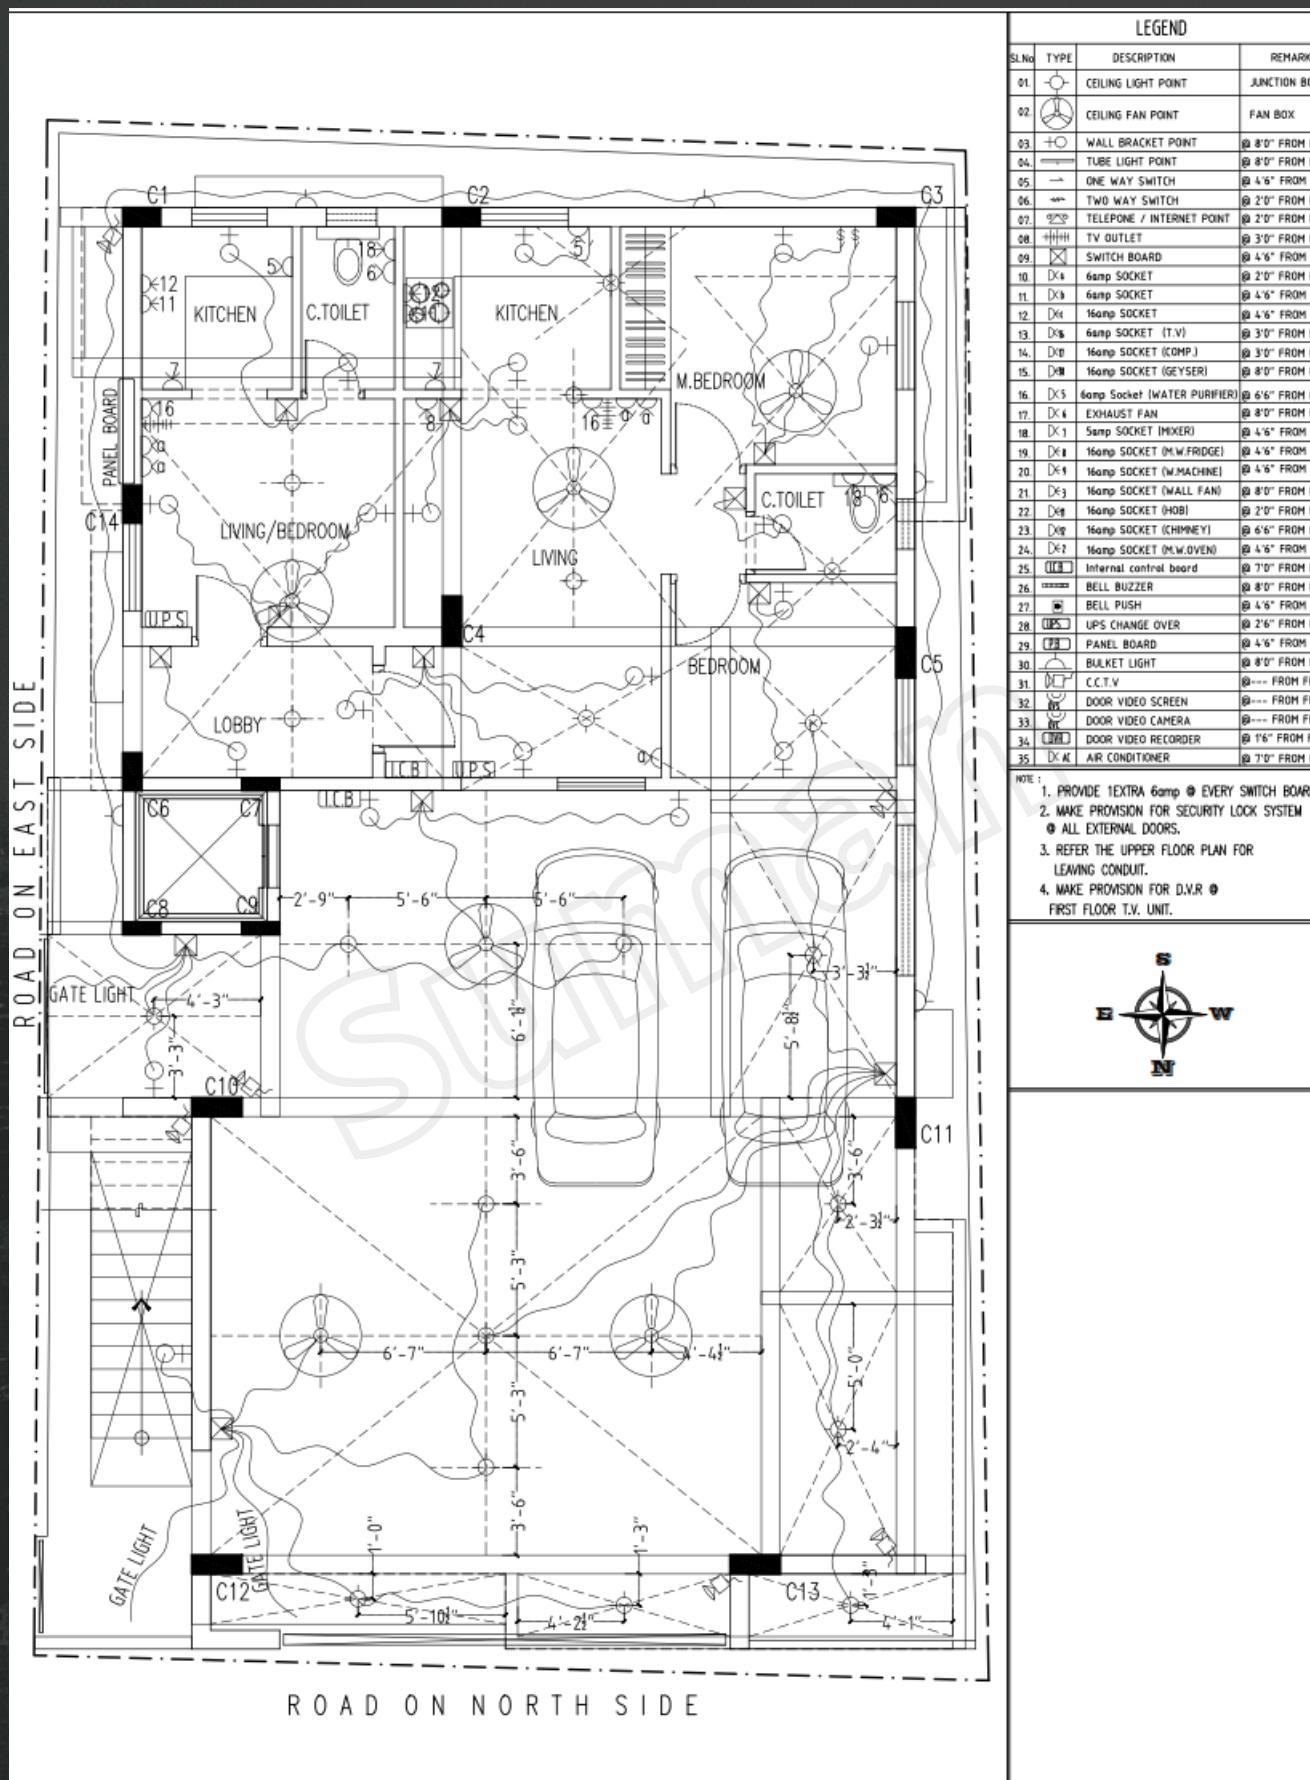



DOOR-WINDOW DRAWING

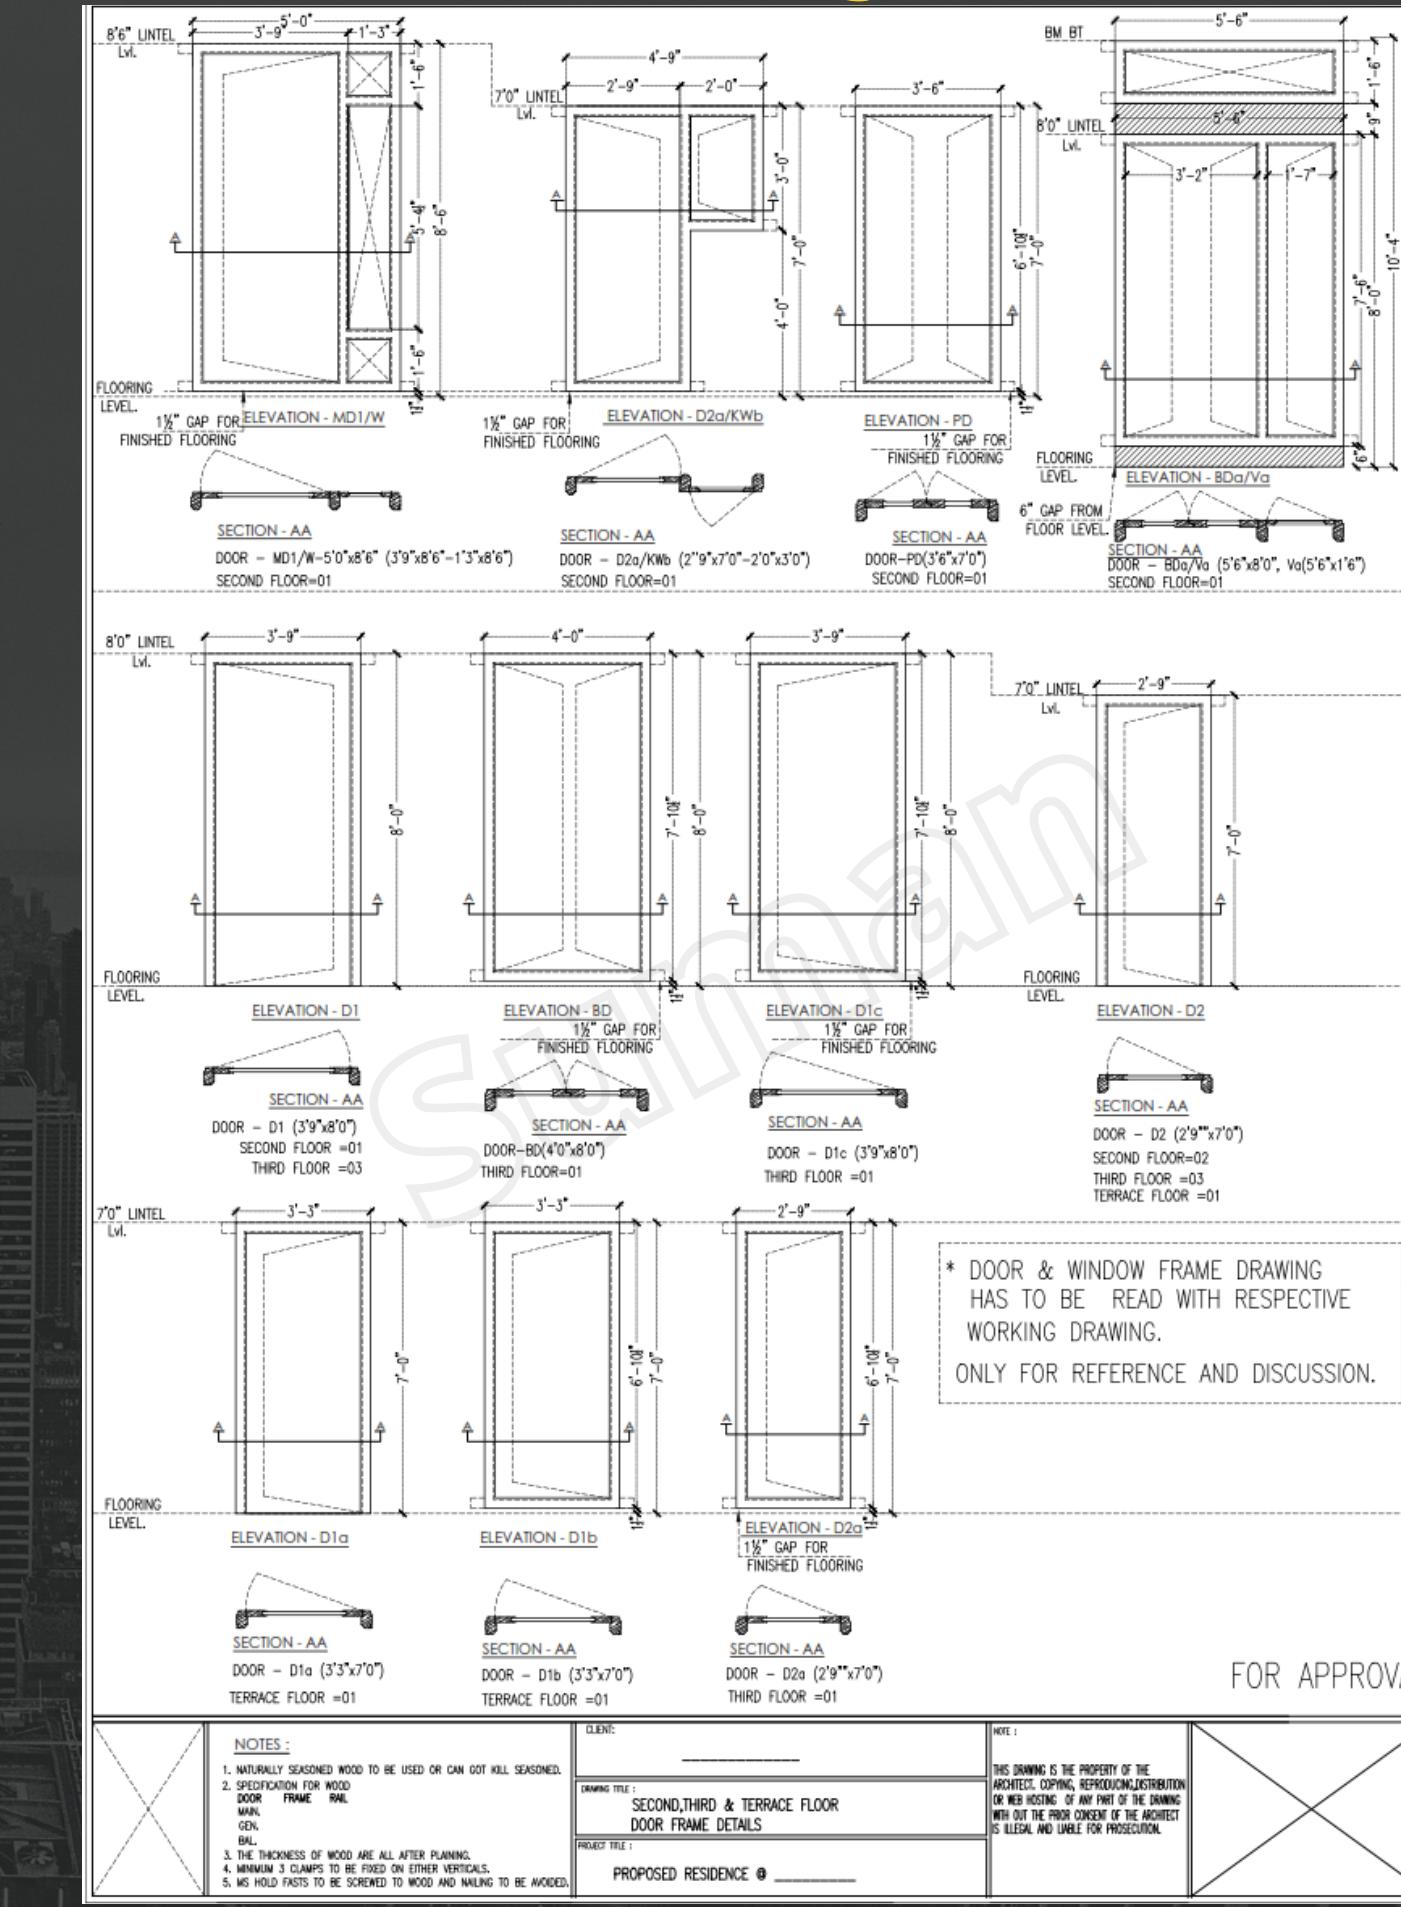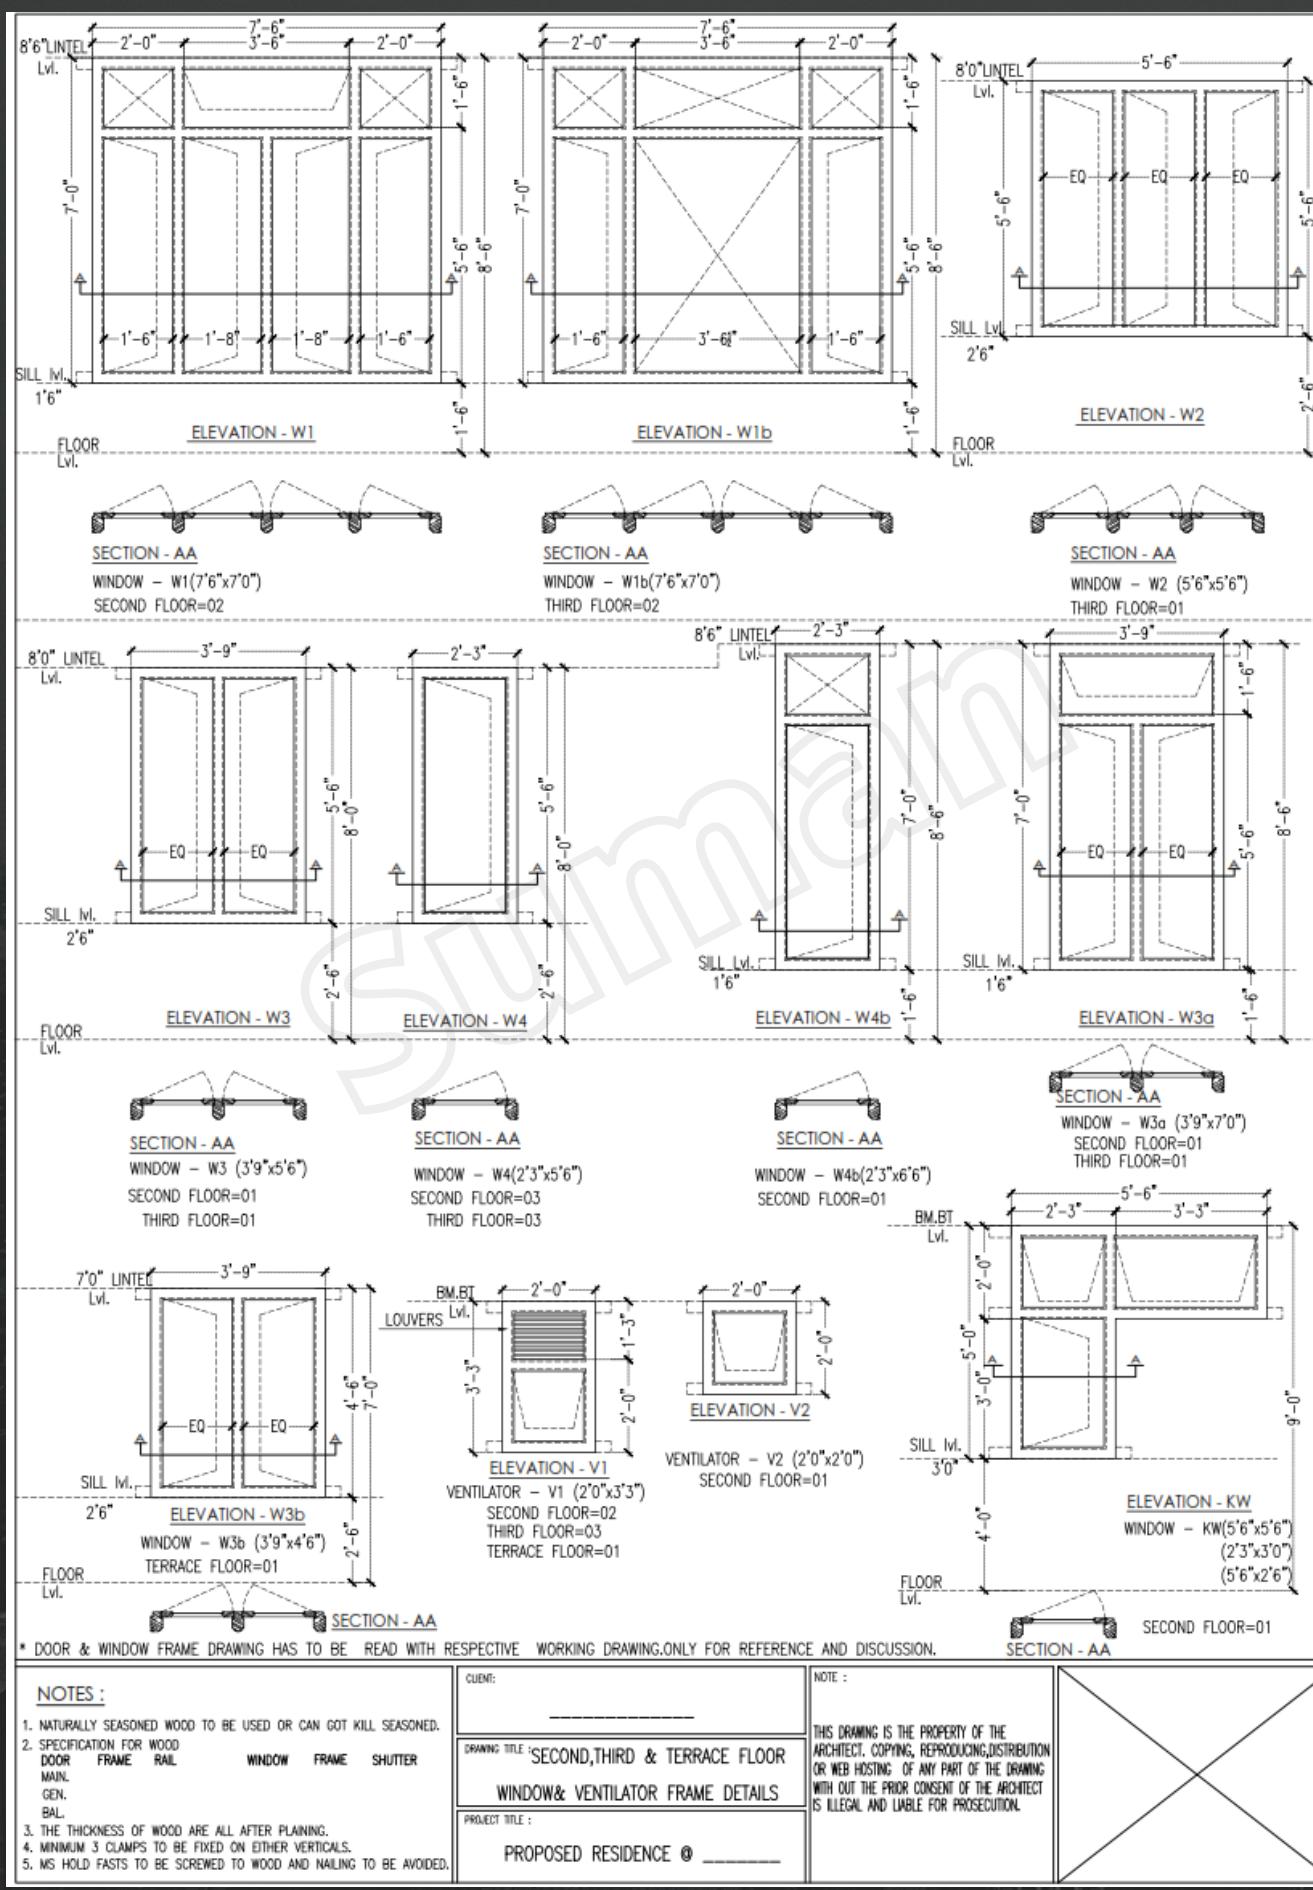


FOR APPROVAL

* DOOR & WINDOW FRAME DRAWING HAS TO BE READ WITH RESPECTIVE WORKING DRAWING.
ONLY FOR REFERENCE AND DISCUSSION.


PLUMBING DRAWING

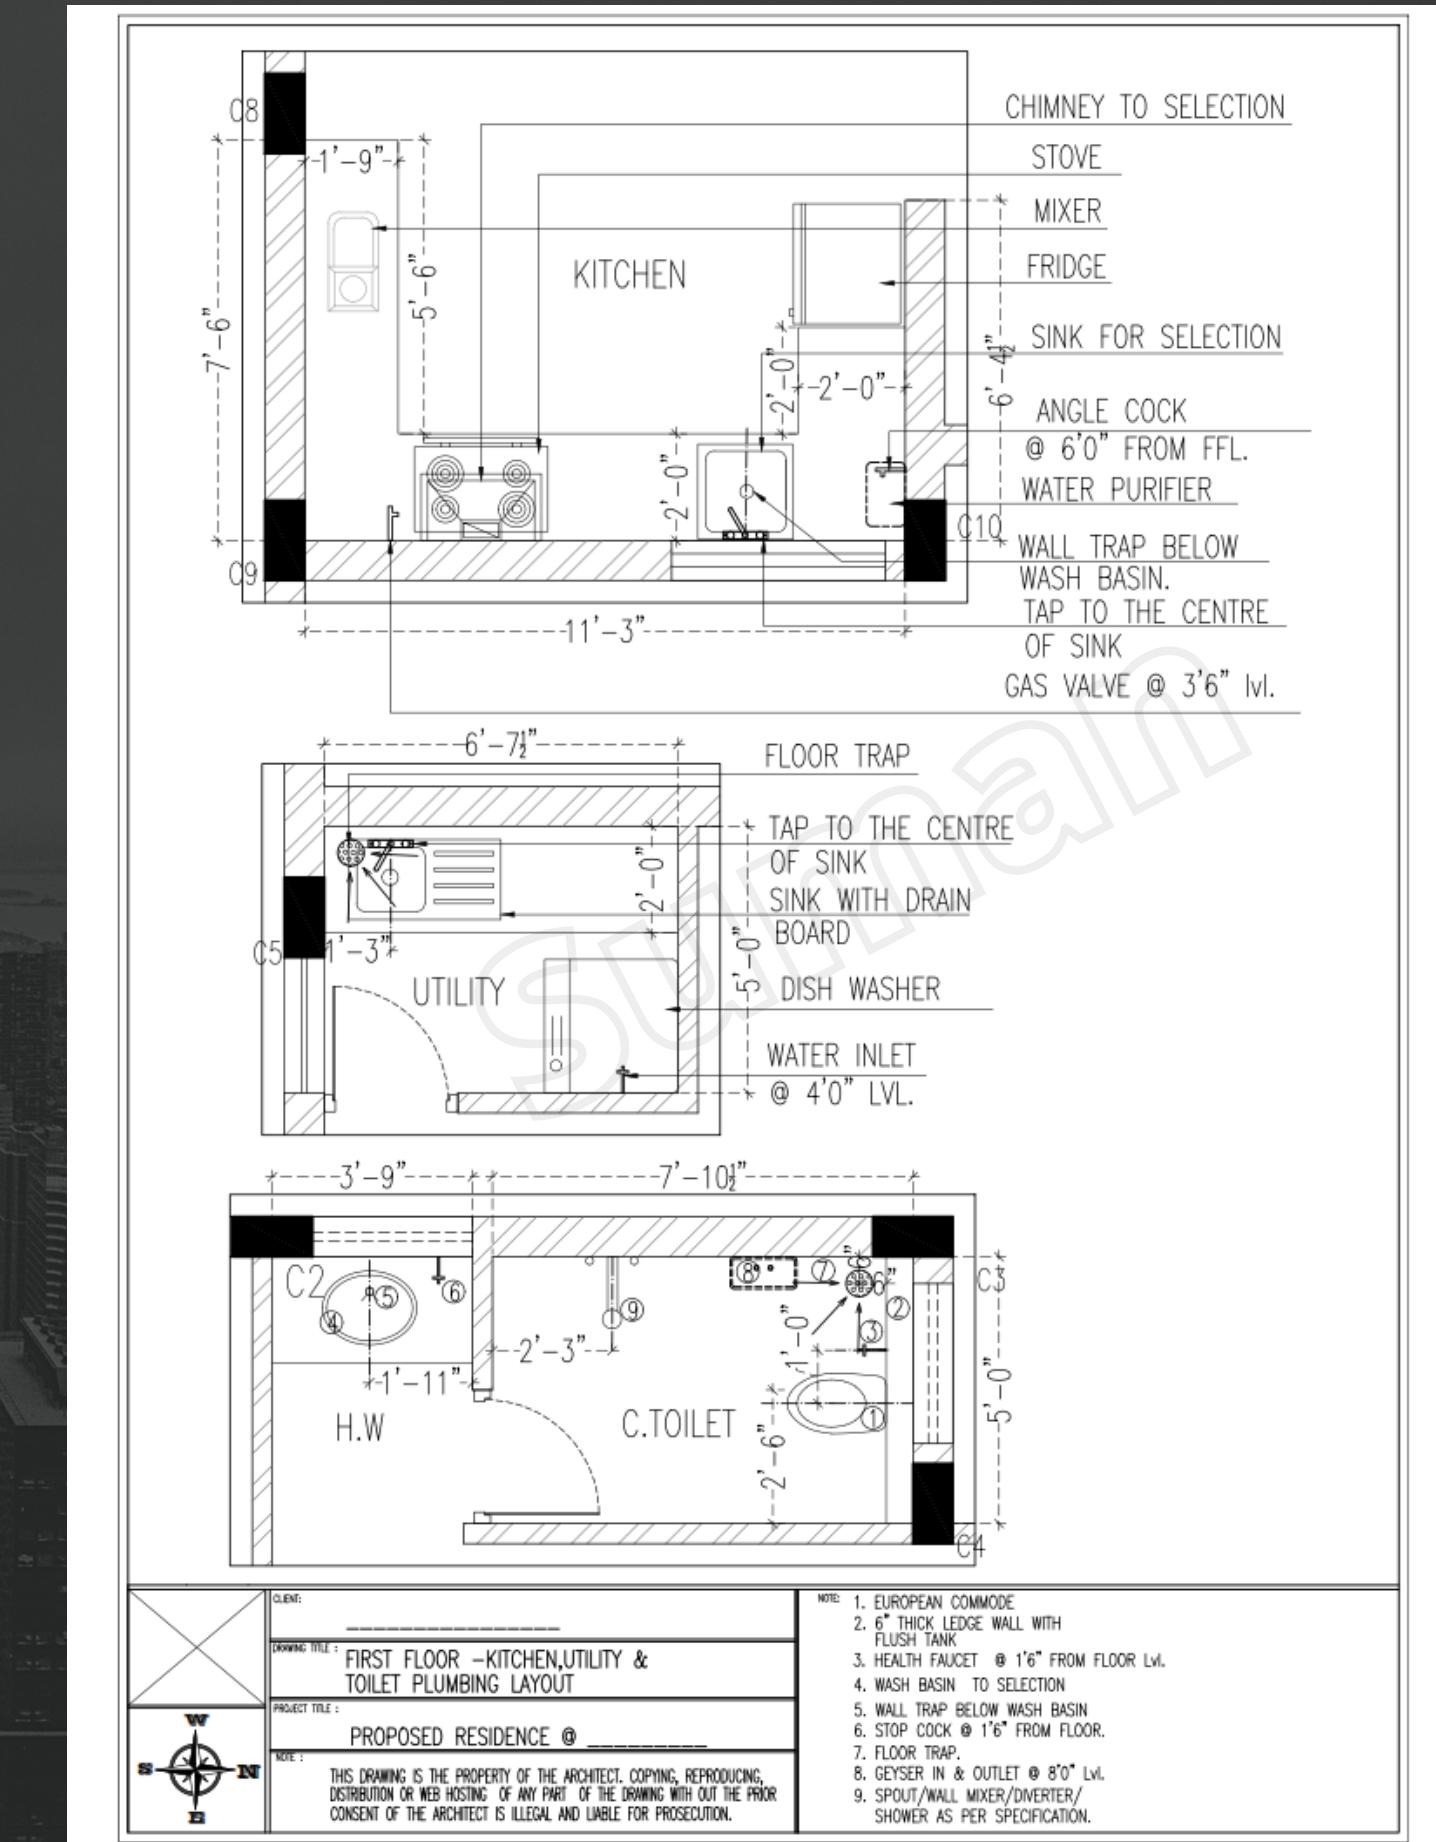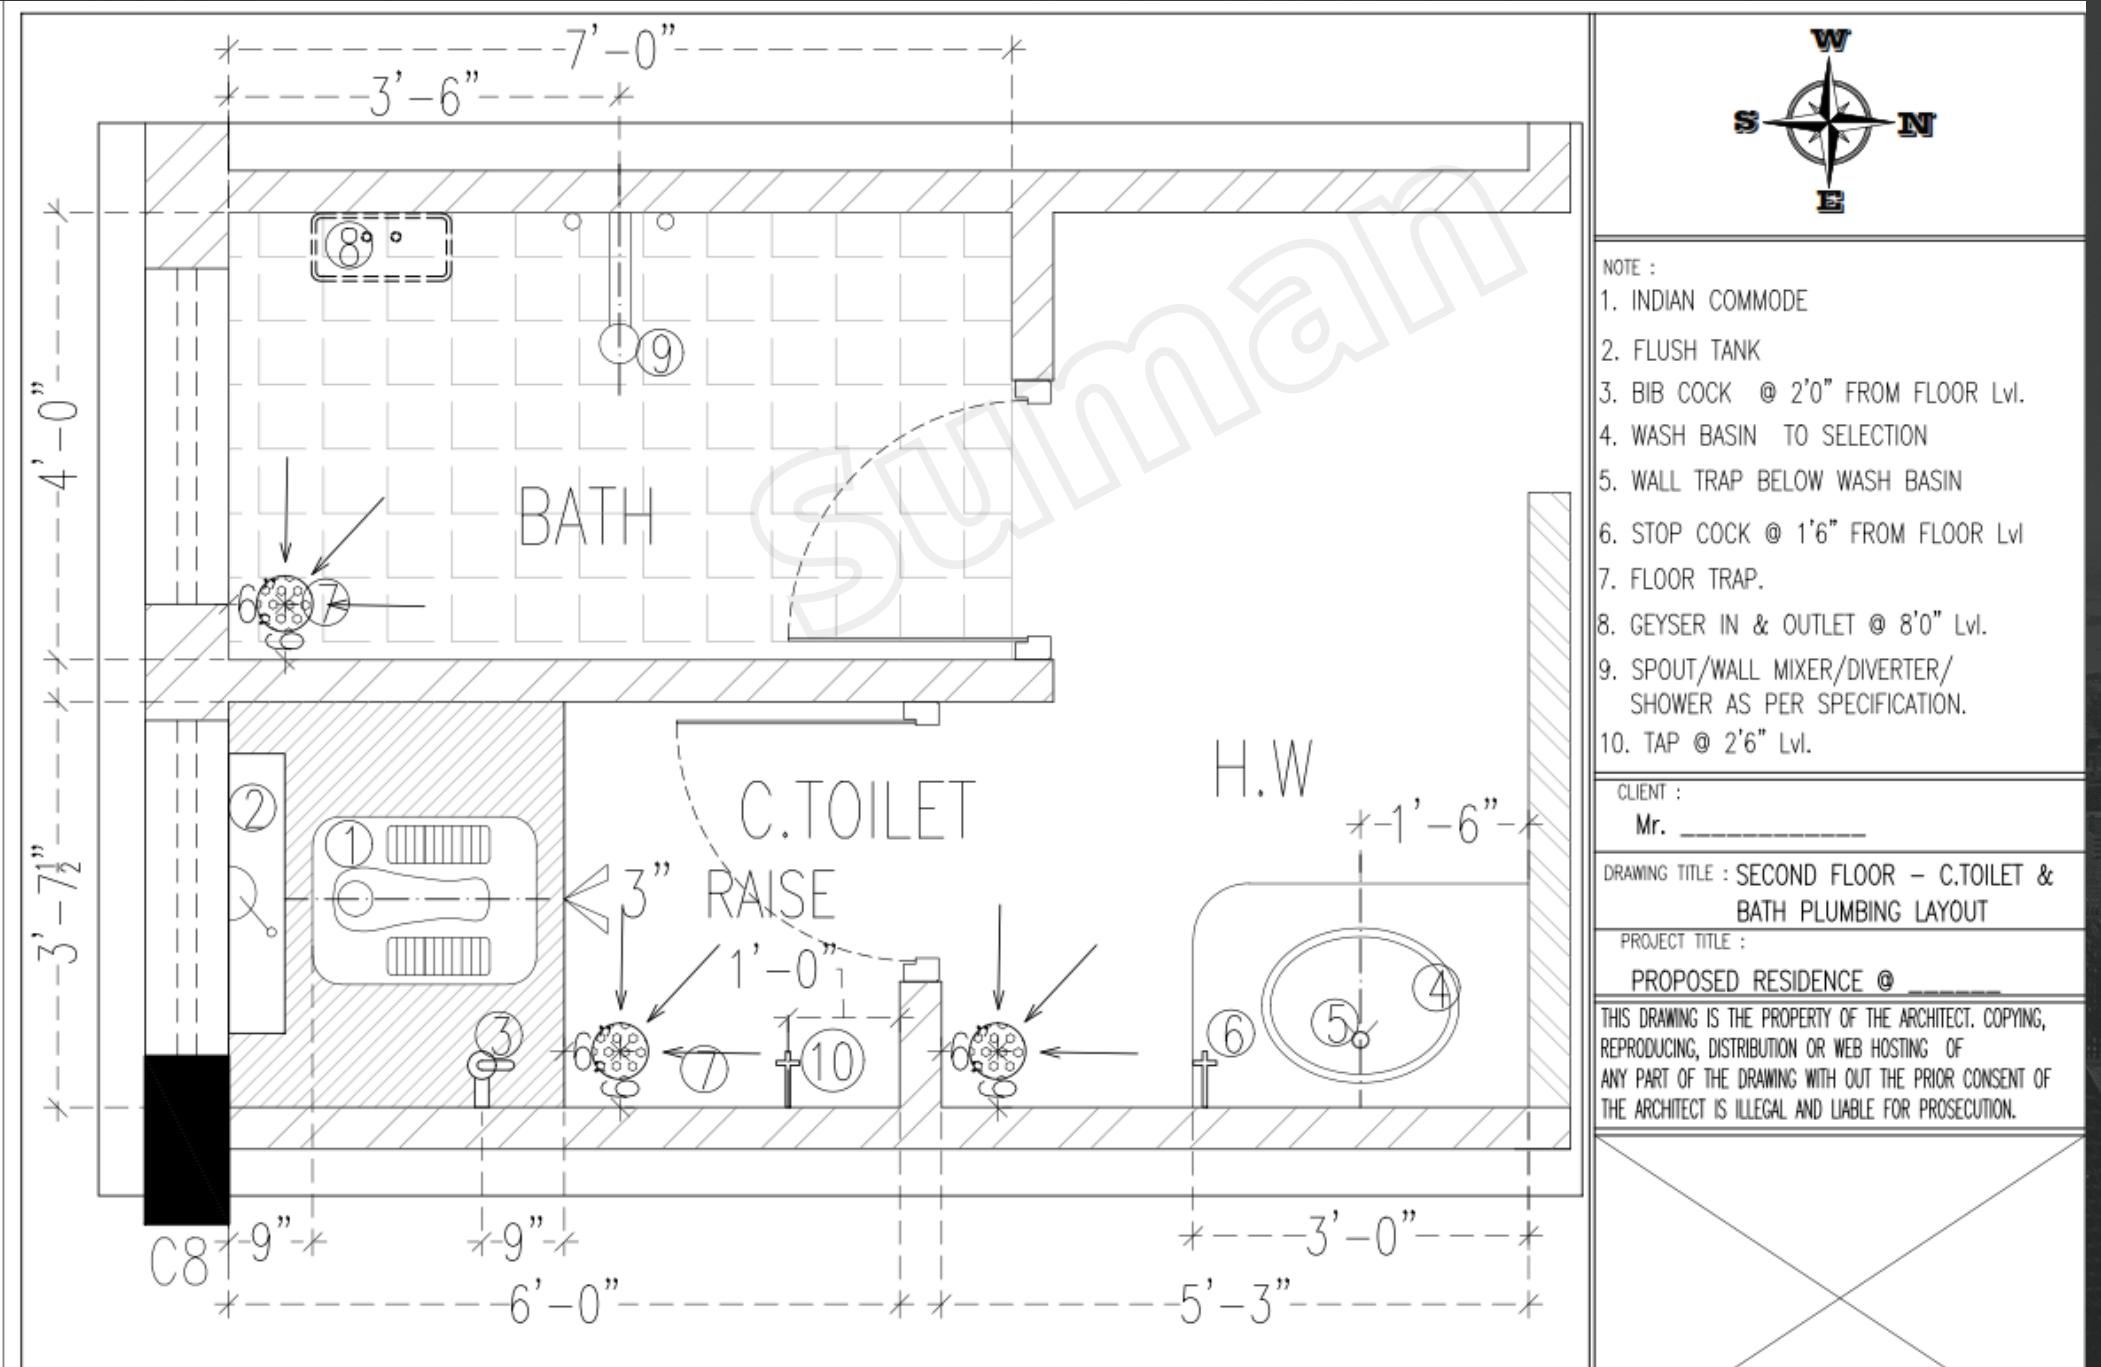



BUILDING PIPELINE DRAWING

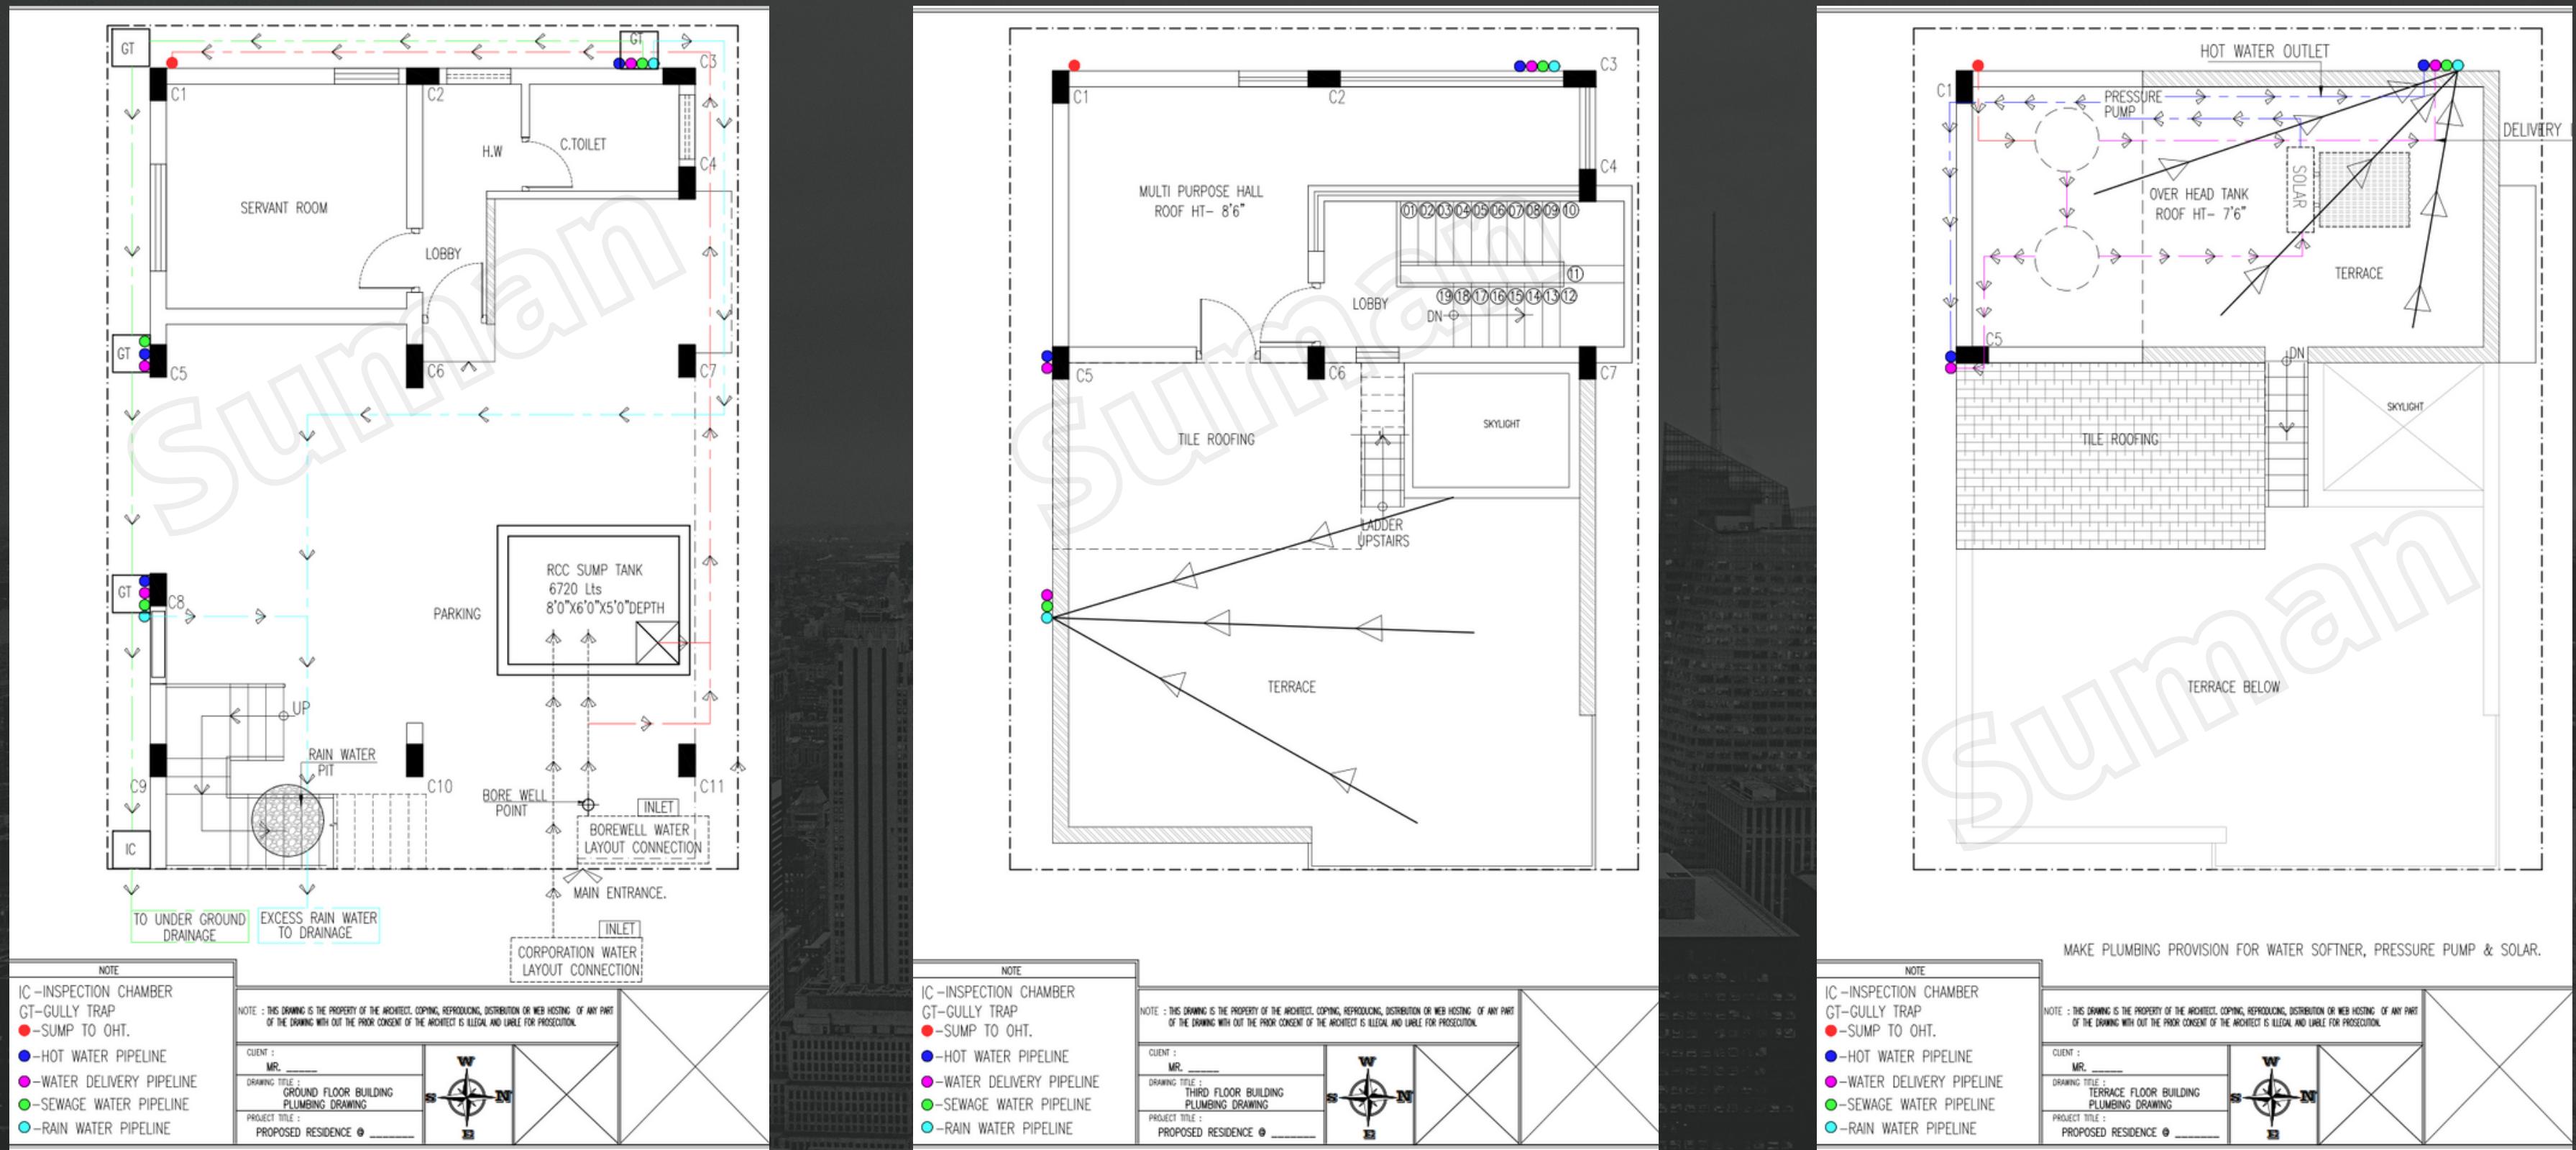



FURNITURE LAYOUT

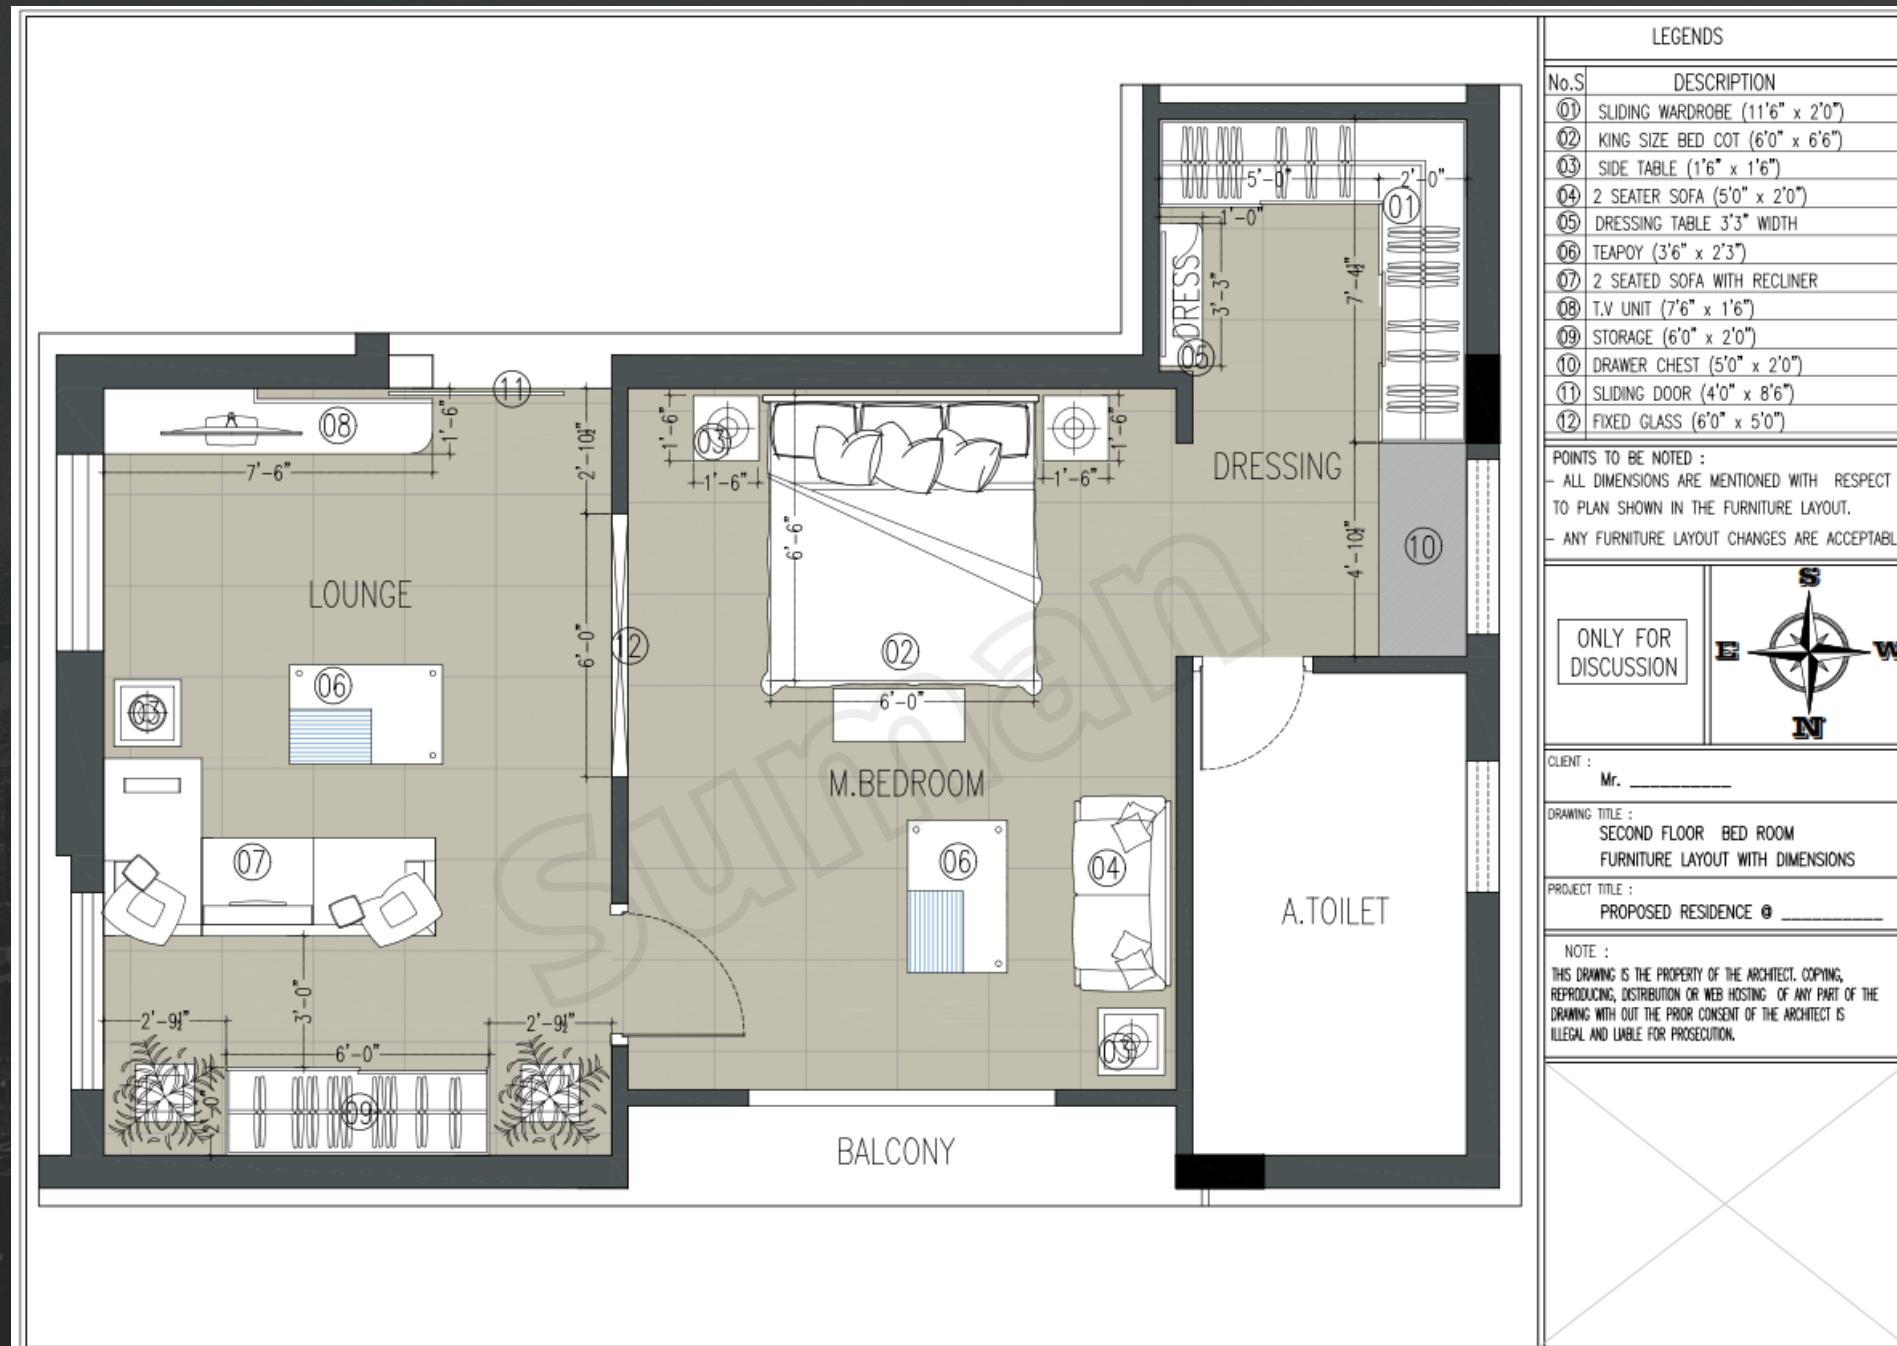


FLOOR ESTIMATION

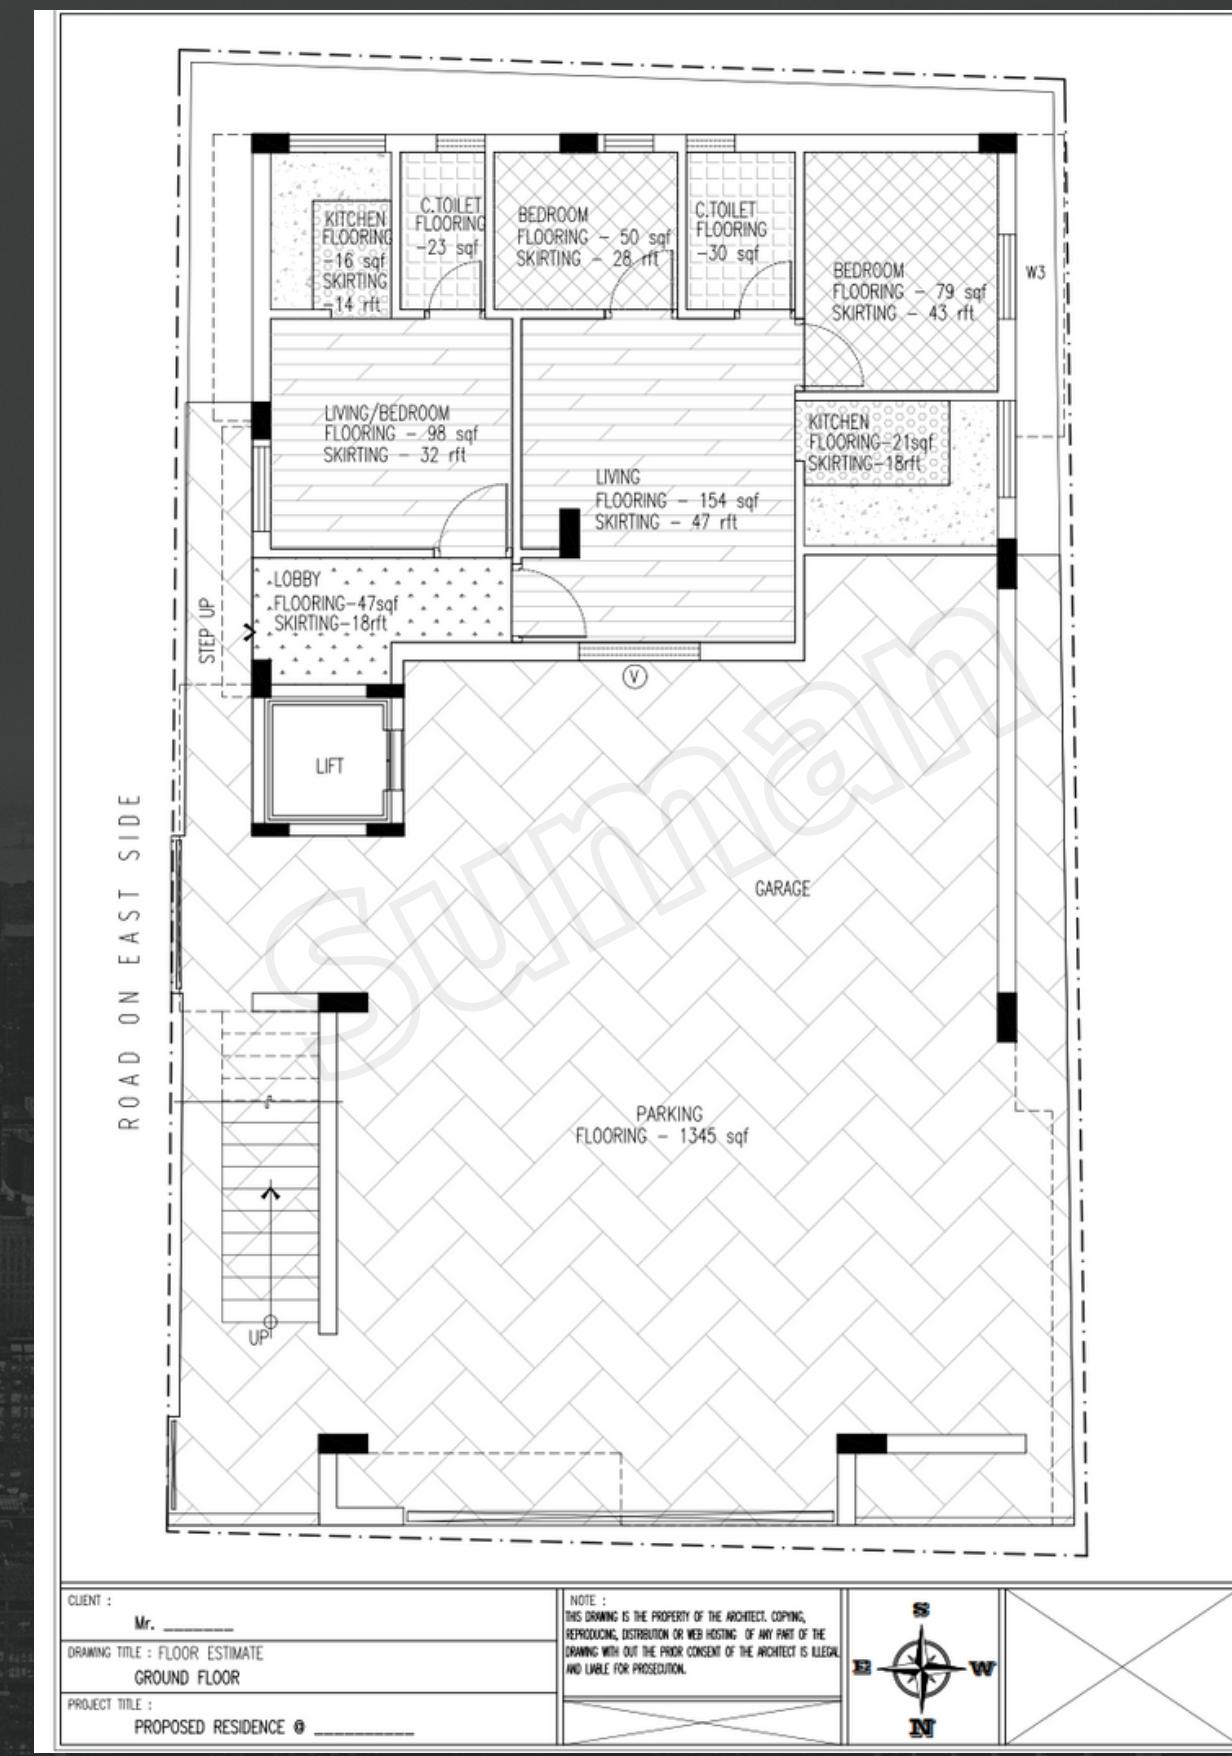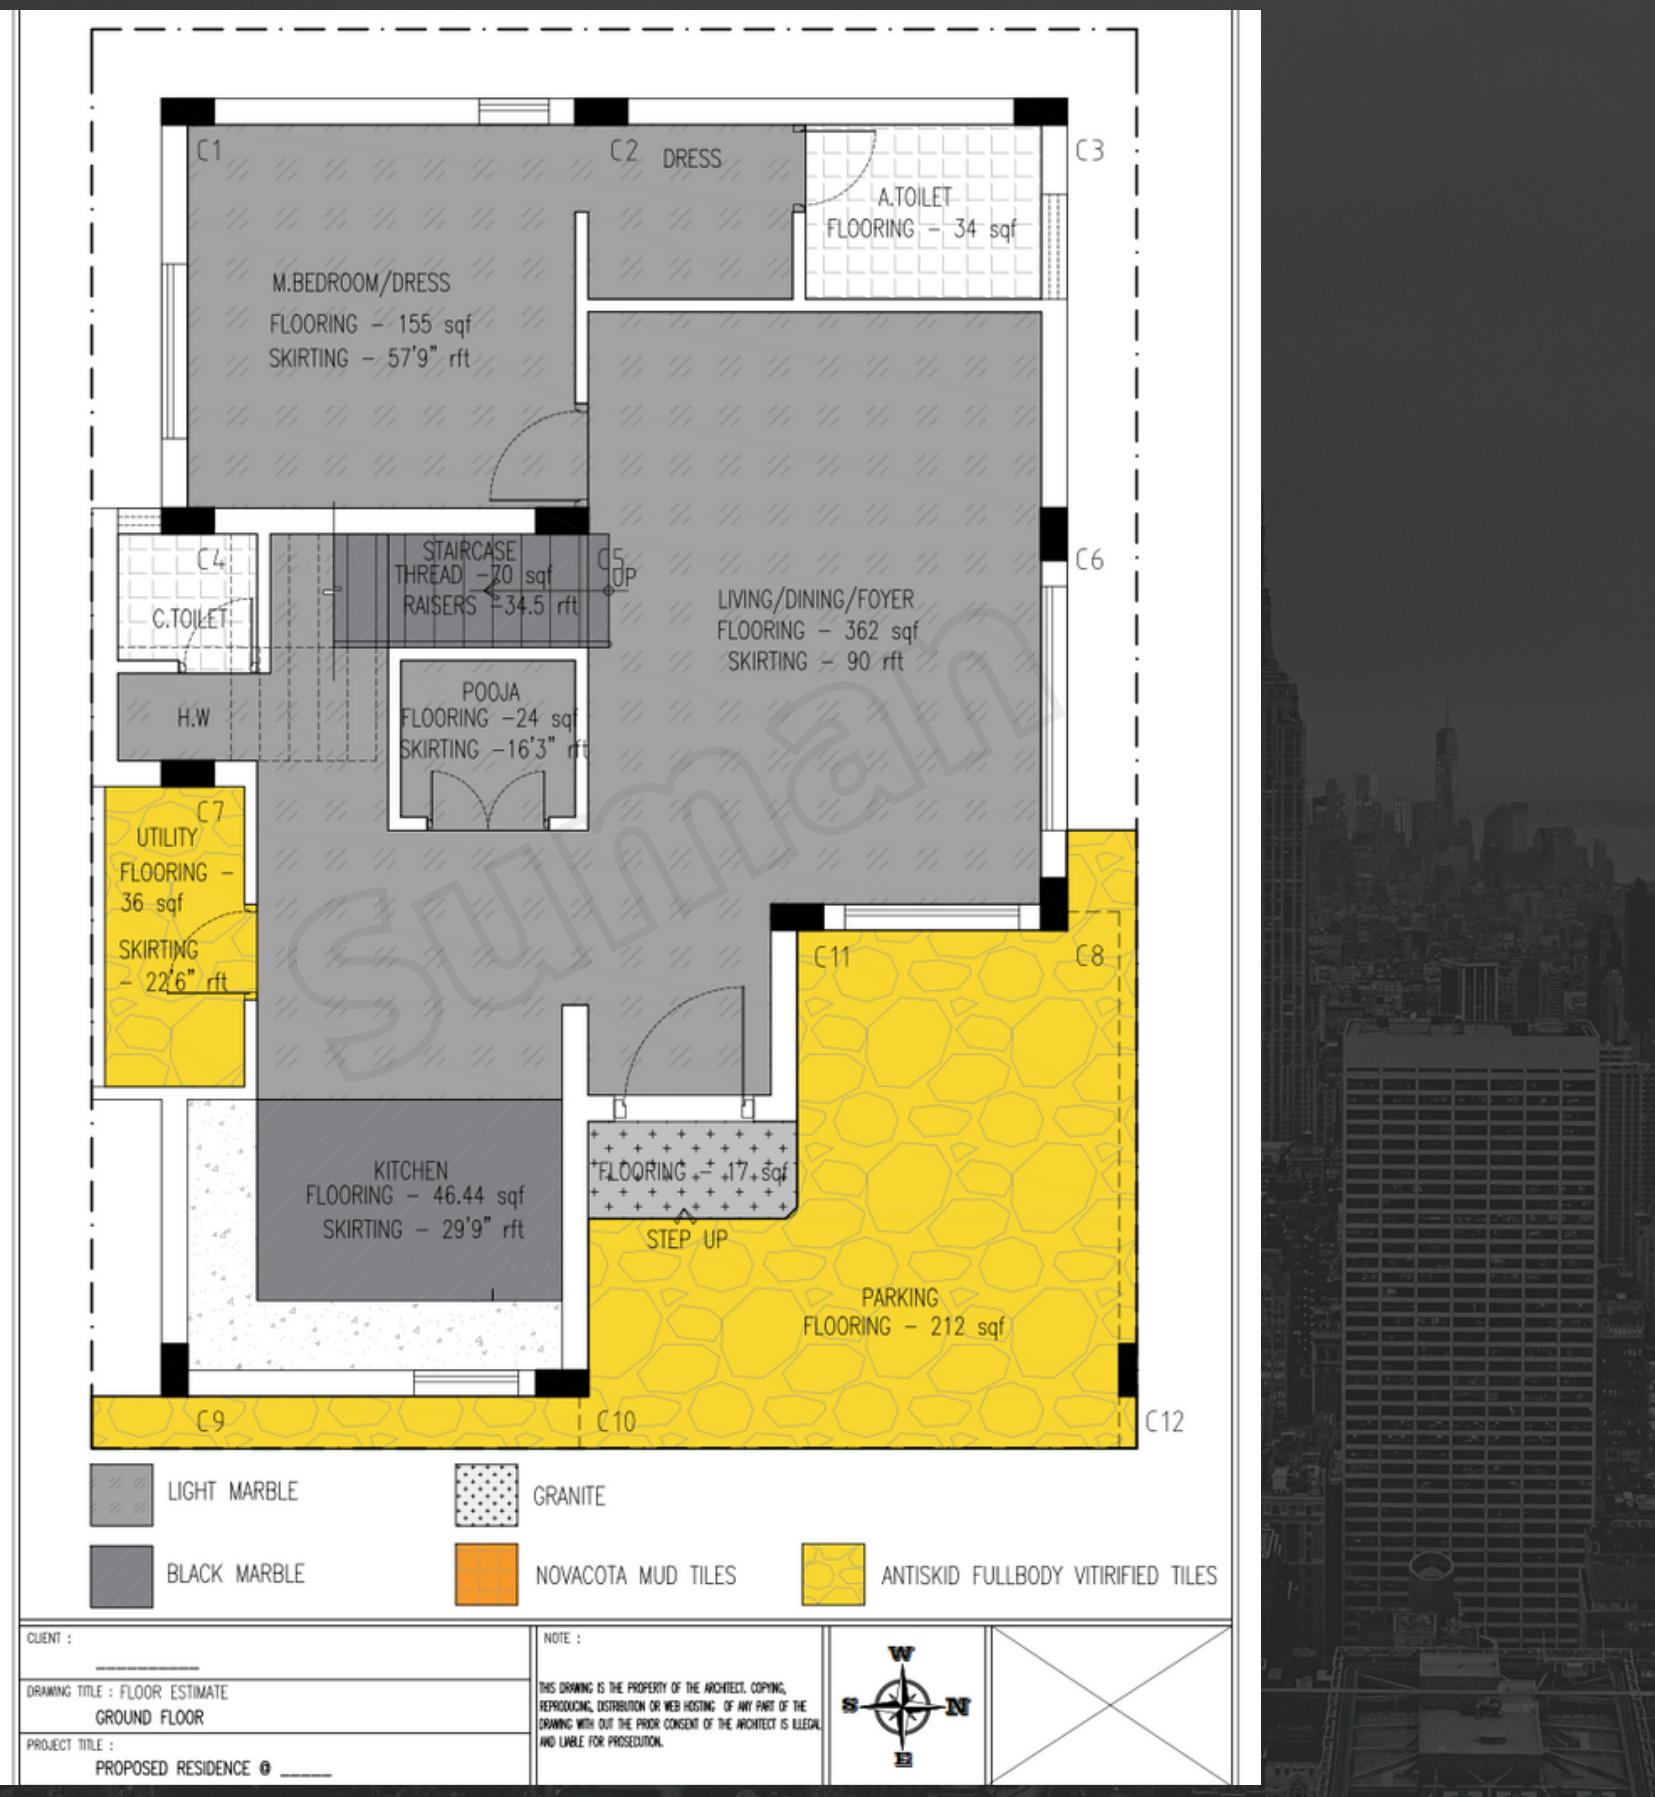

GRILL DESIGNS

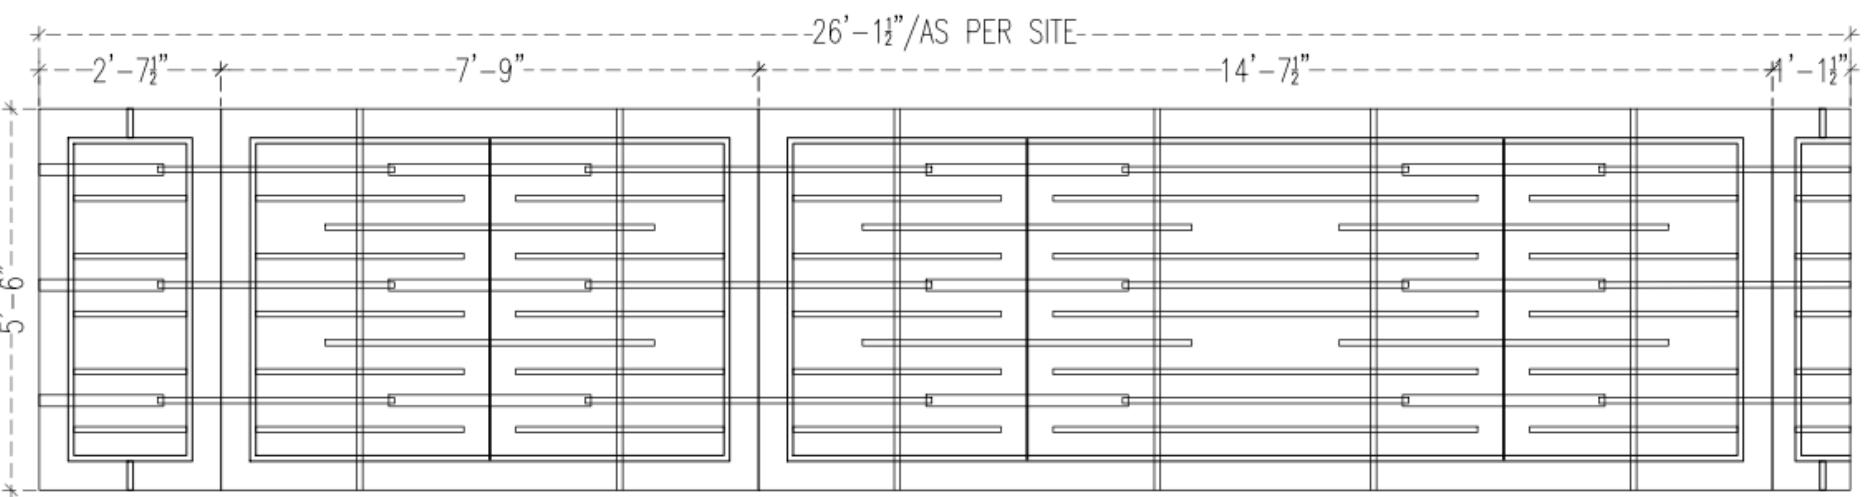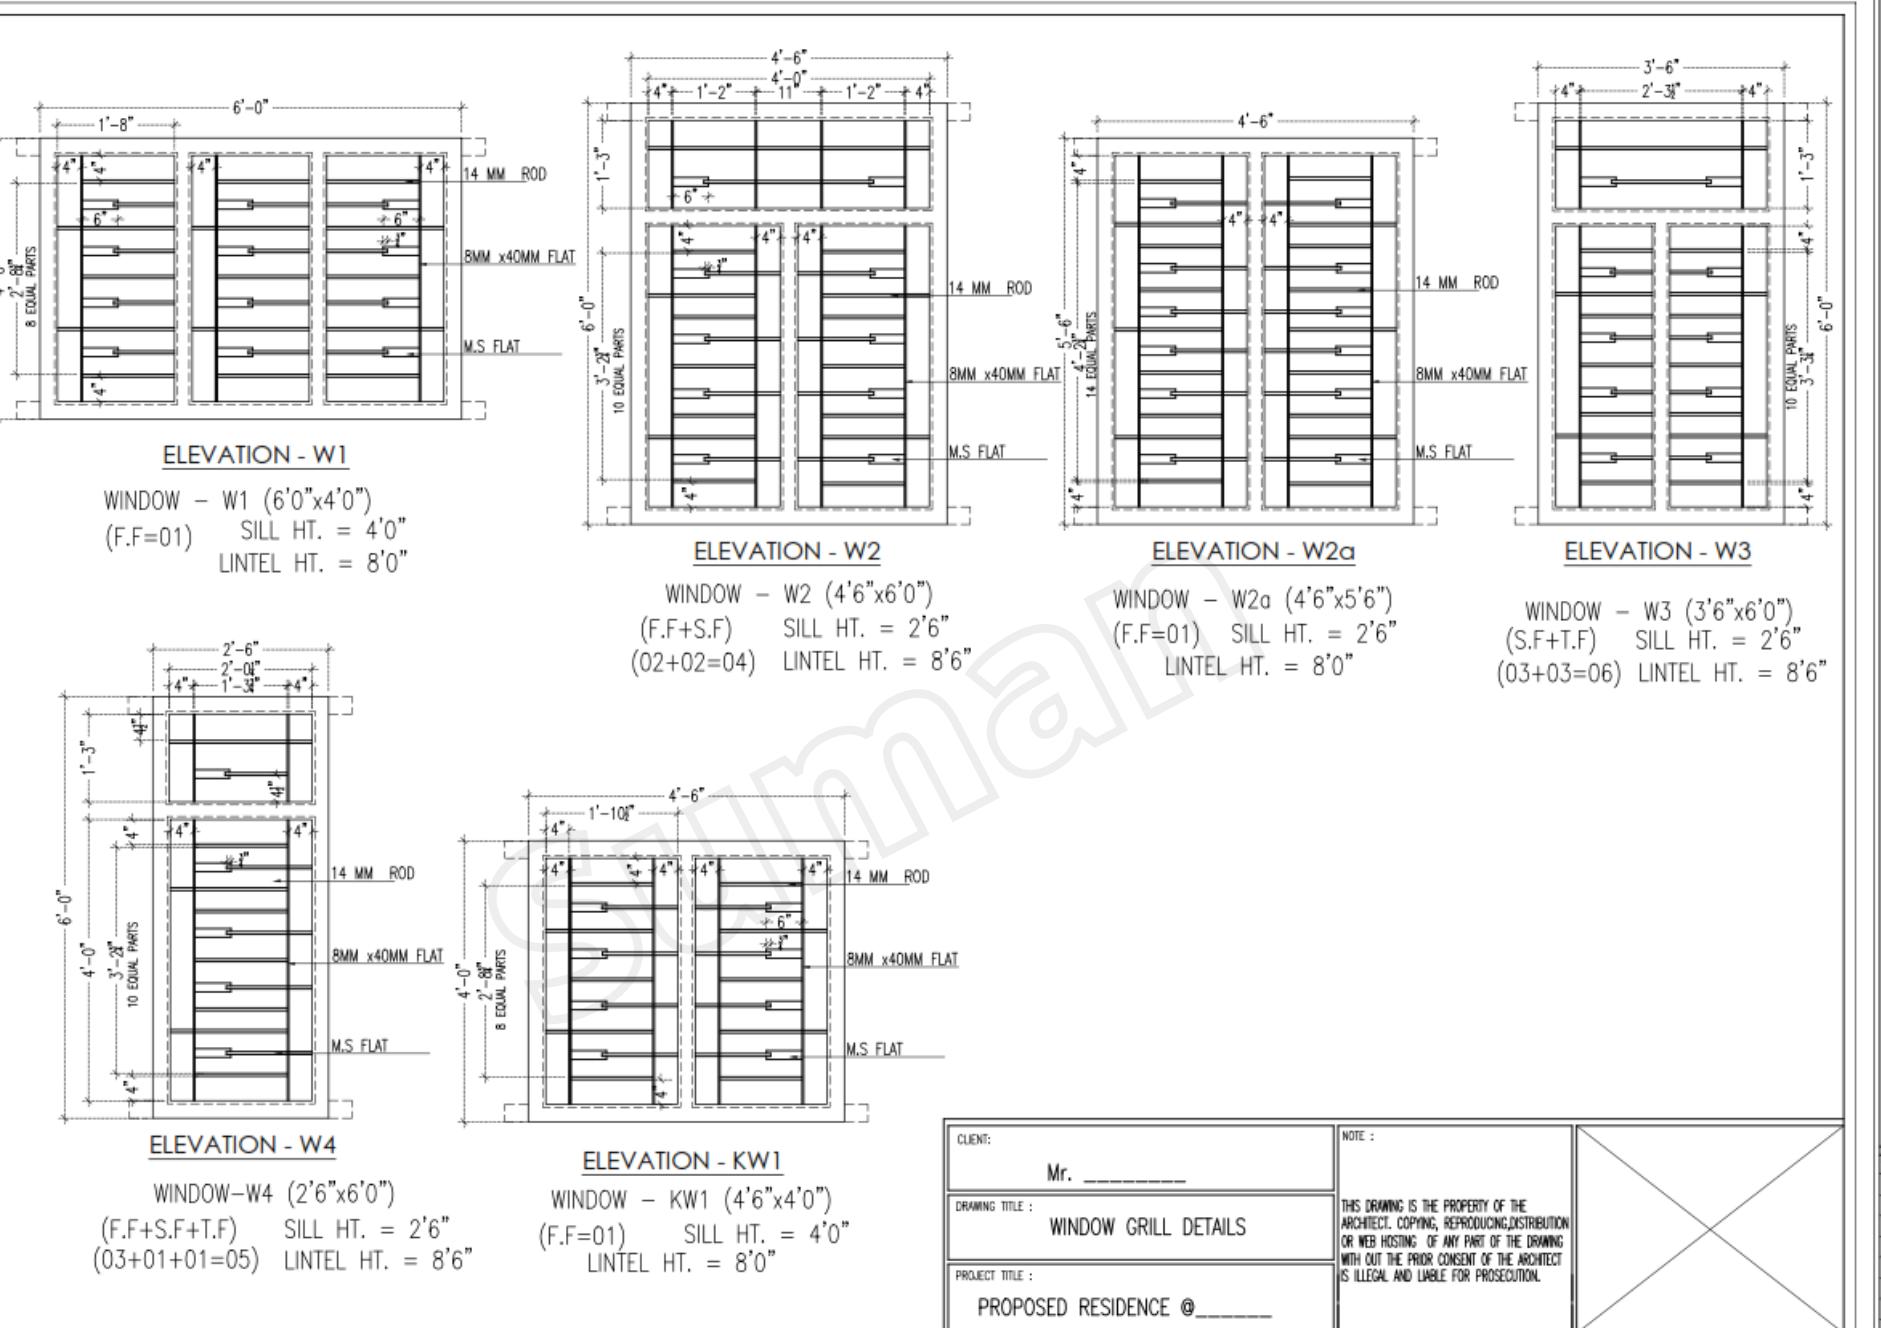

OPTION 01



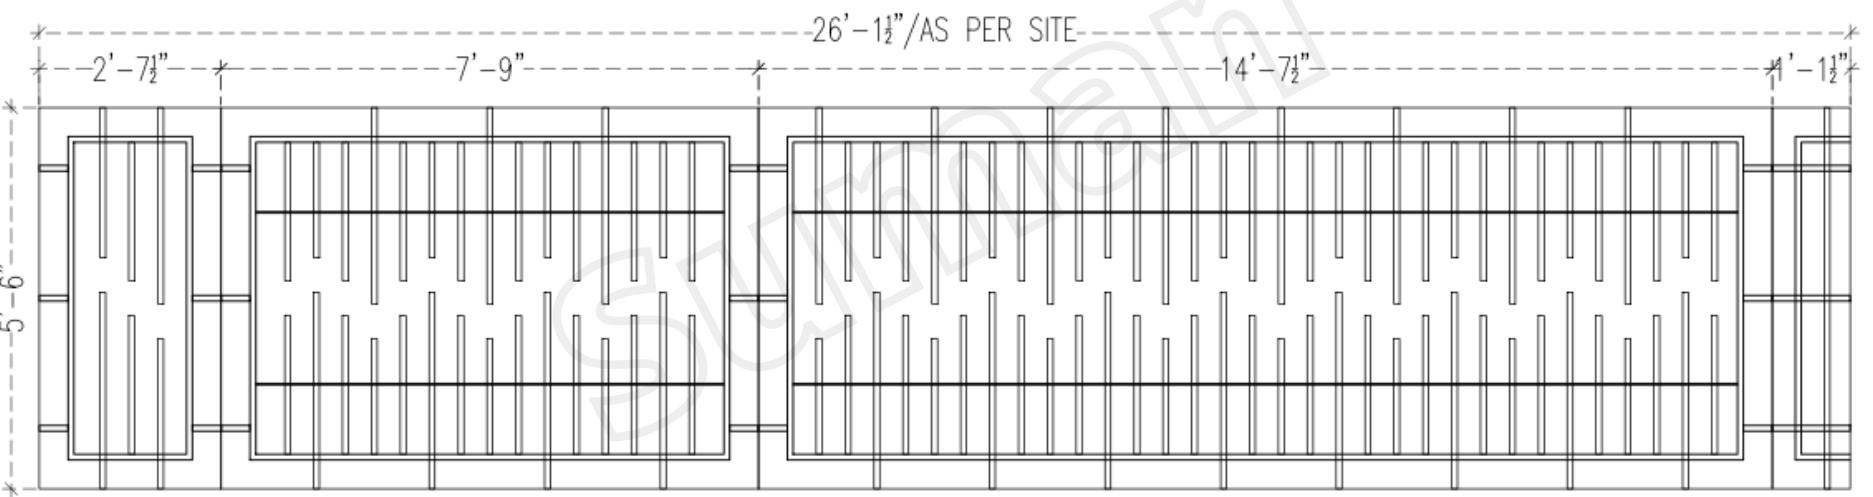


OPTION 02


SI No.	ISSUED BY	ISSUED DATE	SIGN	CLIENT :
				Mr. _____
				DRAWING TITLE : WINDOW GRILL DETAILS
				NOTE : THIS DRAWING IS THE PROPERTY OF THE ARCHITECT. COPYING, REPRODUCING, DISTRIBUTION OR WEB HOSTING OF ANY PART OF THE DRAWING WITHOUT THE PRIOR CONSENT OF THE ARCHITECT IS ILLEGAL AND LIABLE FOR PROSECUTION.
				PROJECT TITLE : PROPOSED RESIDENCE @ _____

SI No.	ISSUED BY	ISSUED DATE	SIGN	CLIENT :
				Mr. _____
				DRAWING TITLE : GRILL DESIGN OPTIONS
				NOTE : THIS DRAWING IS THE PROPERTY OF THE ARCHITECT. COPYING, REPRODUCING, DISTRIBUTION OR WEB HOSTING OF ANY PART OF THE DRAWING WITHOUT THE PRIOR CONSENT OF THE ARCHITECT IS ILLEGAL AND LIABLE FOR PROSECUTION.
				PROJECT TITLE : PROPOSED RESIDENCE @ _____




TILE LAYOUT DESIGN

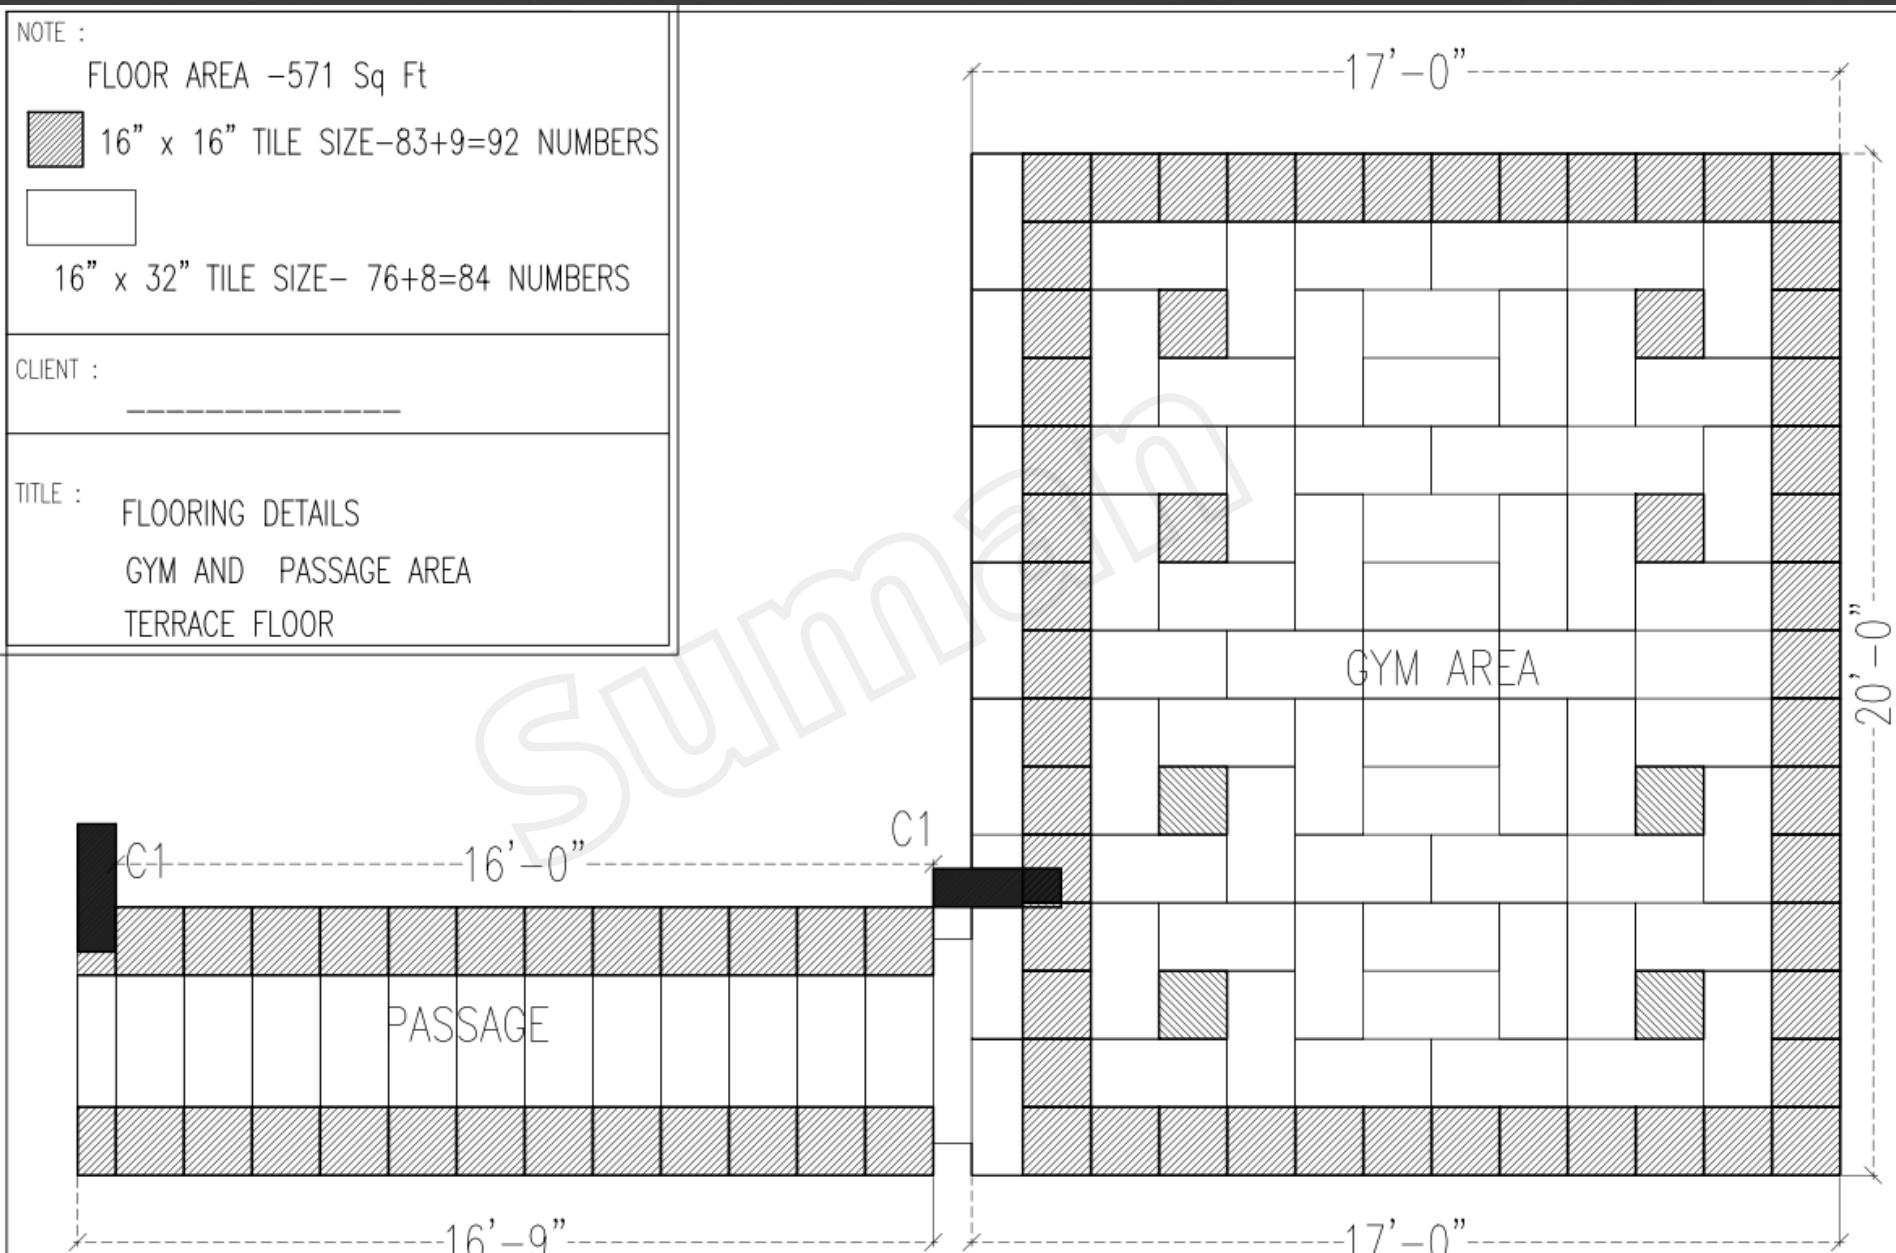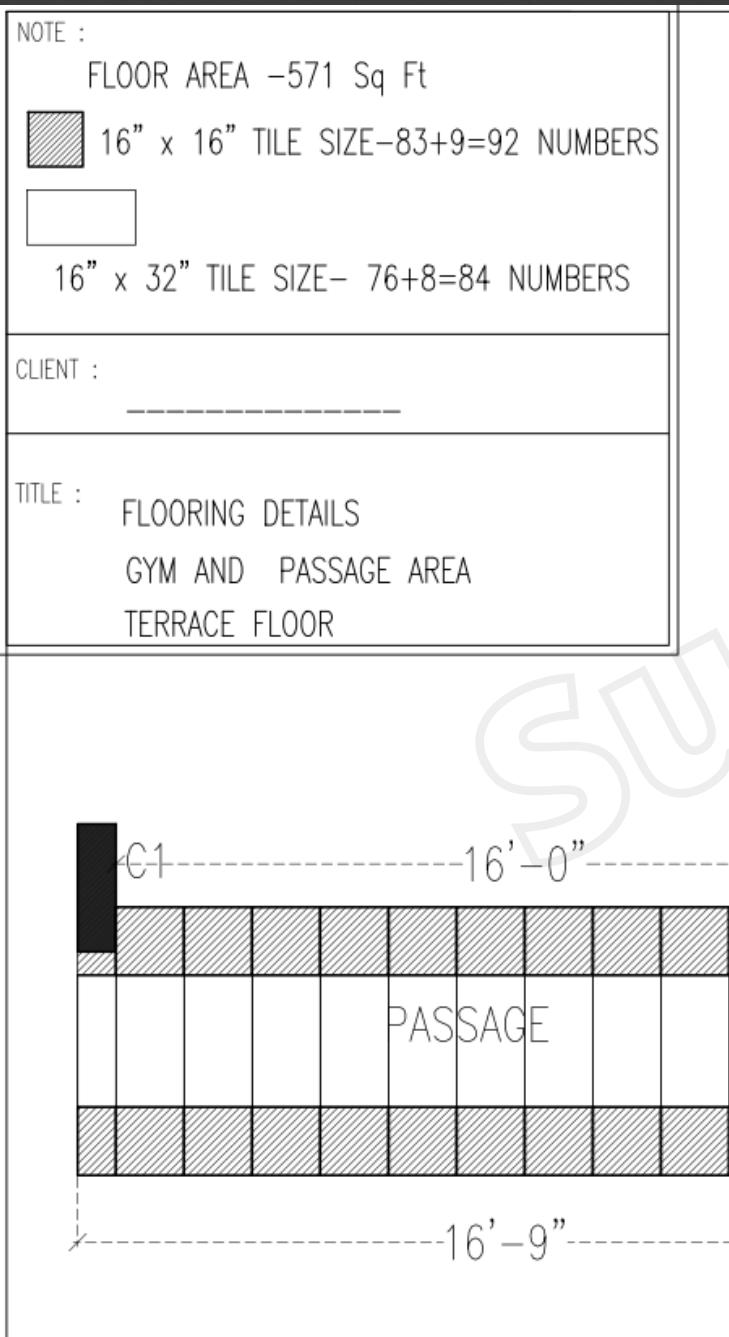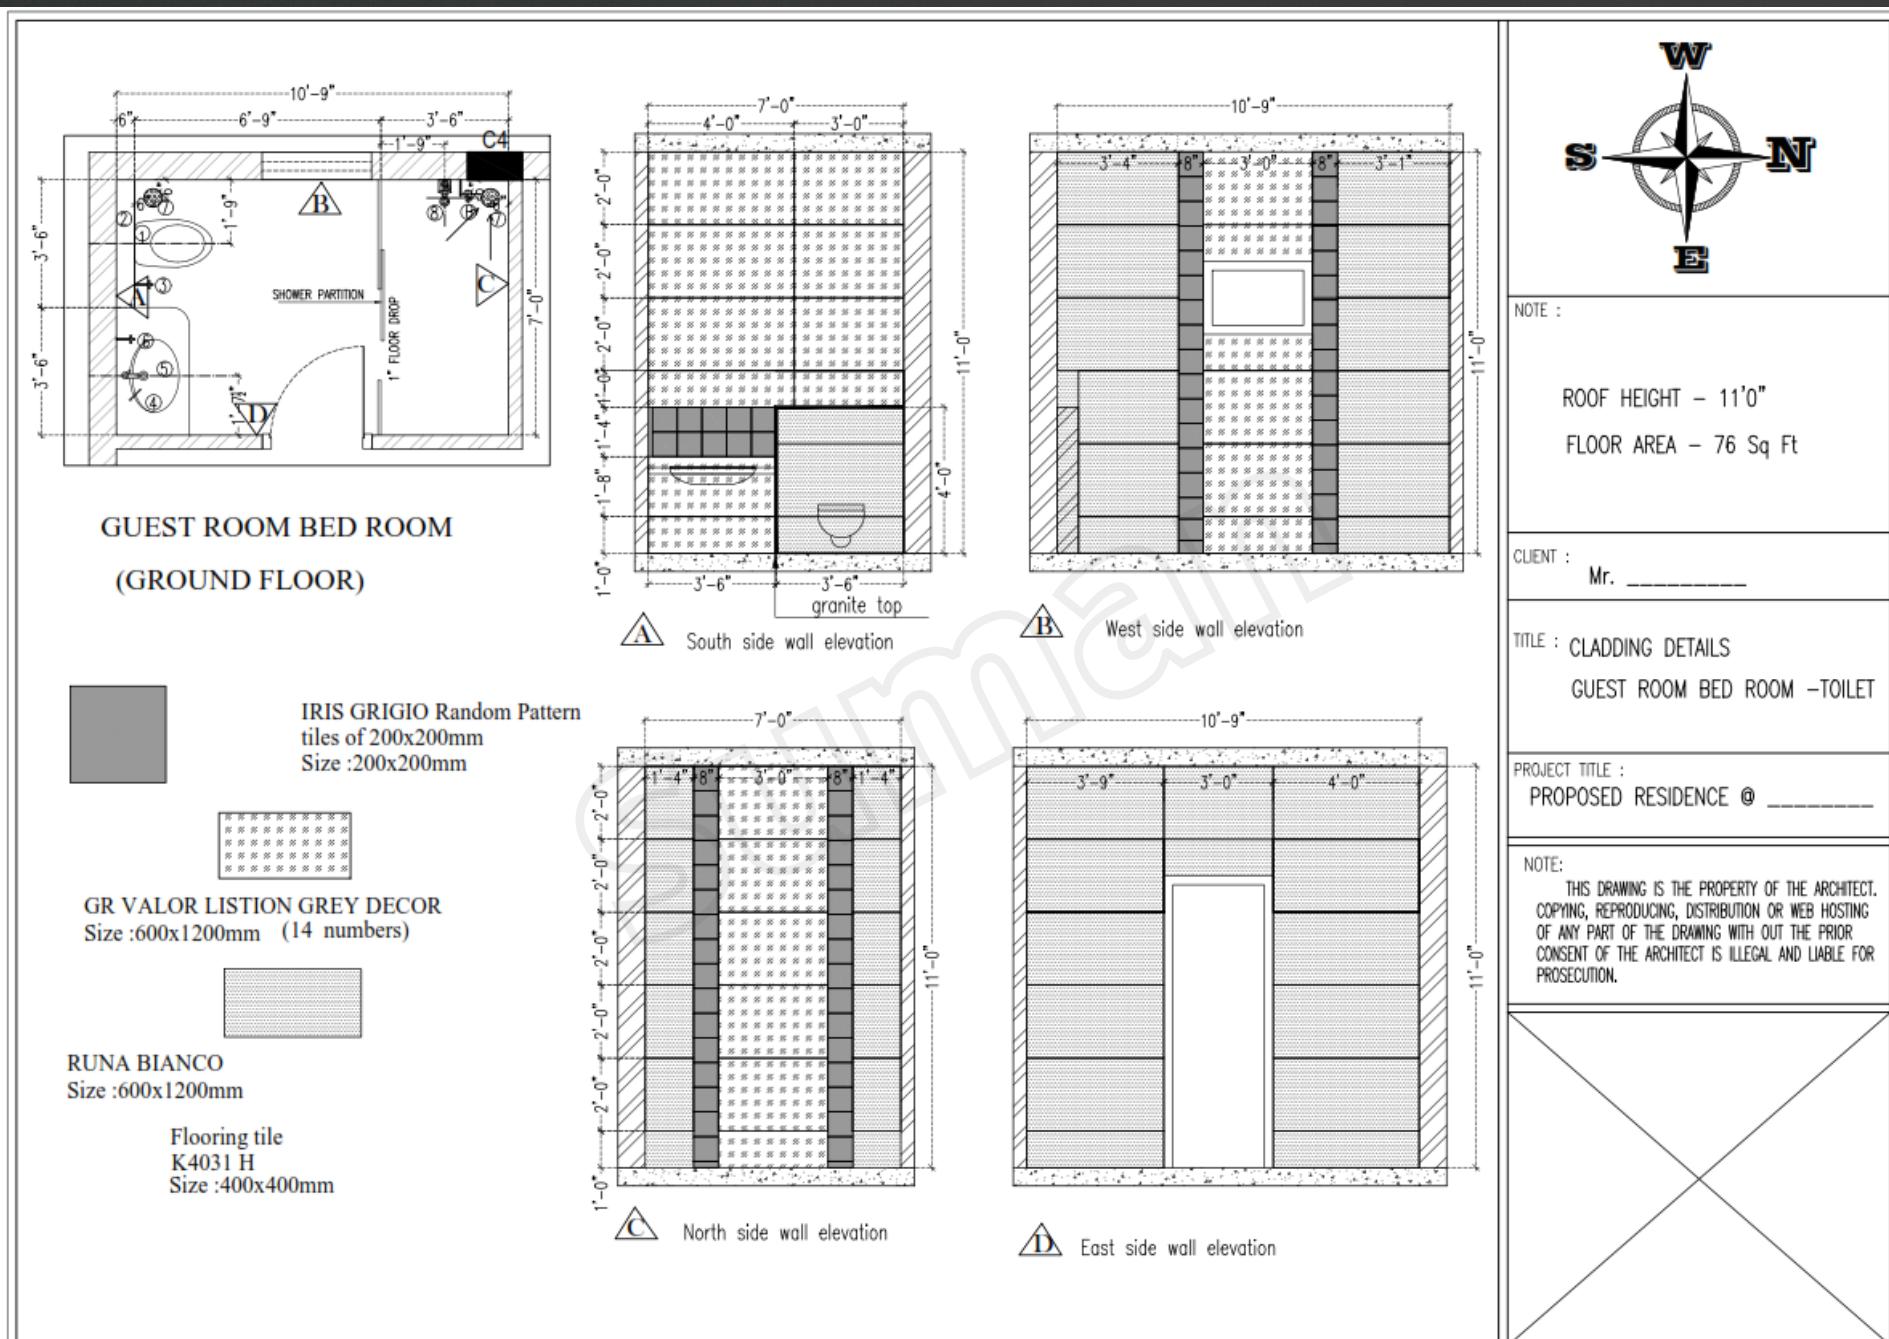


GENERAL TOILET LAYOUT

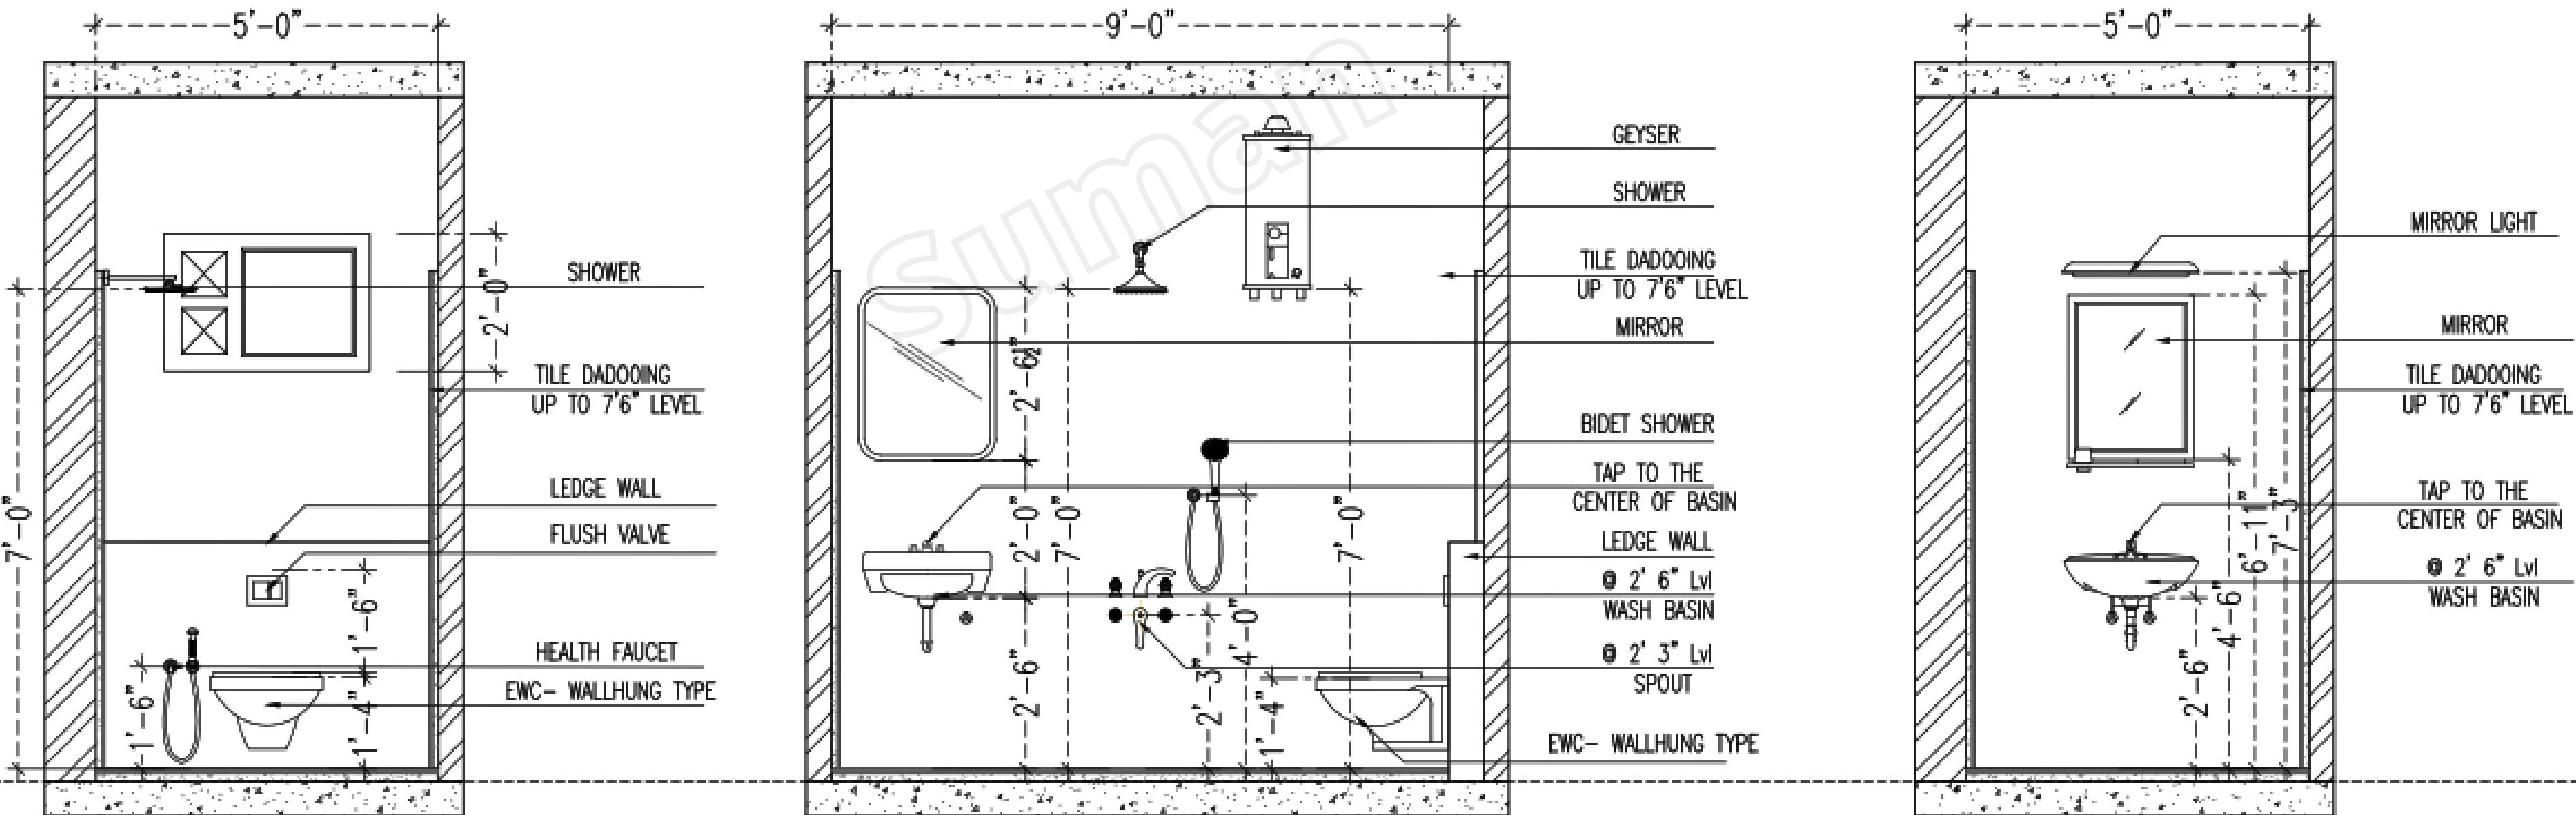


GENERAL ELECTRICAL LAYOUT

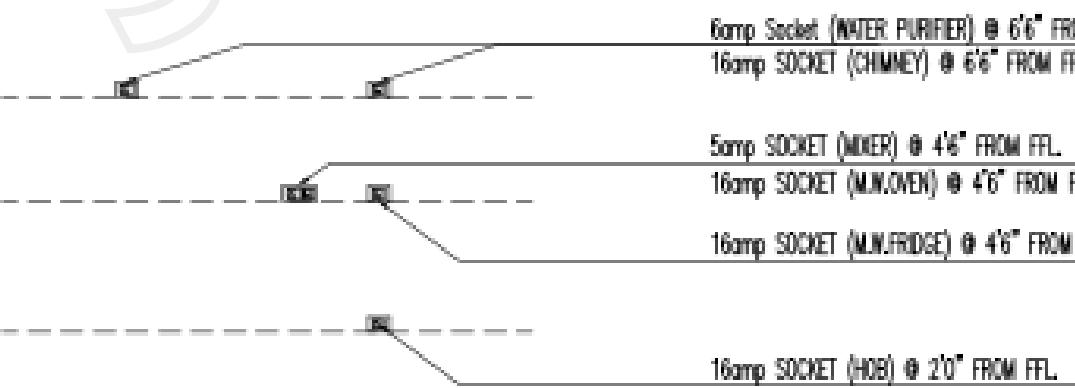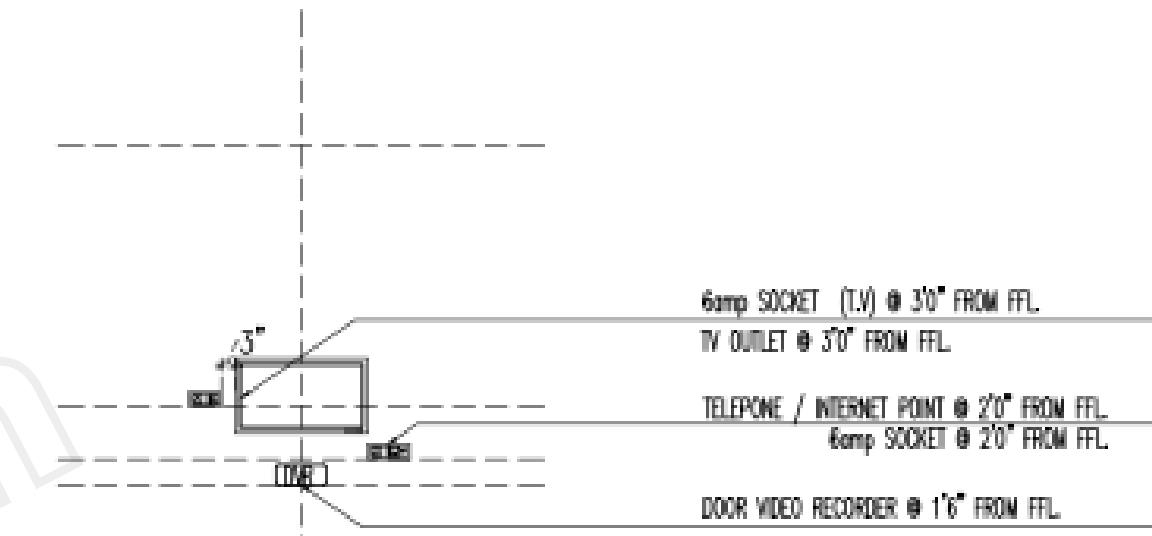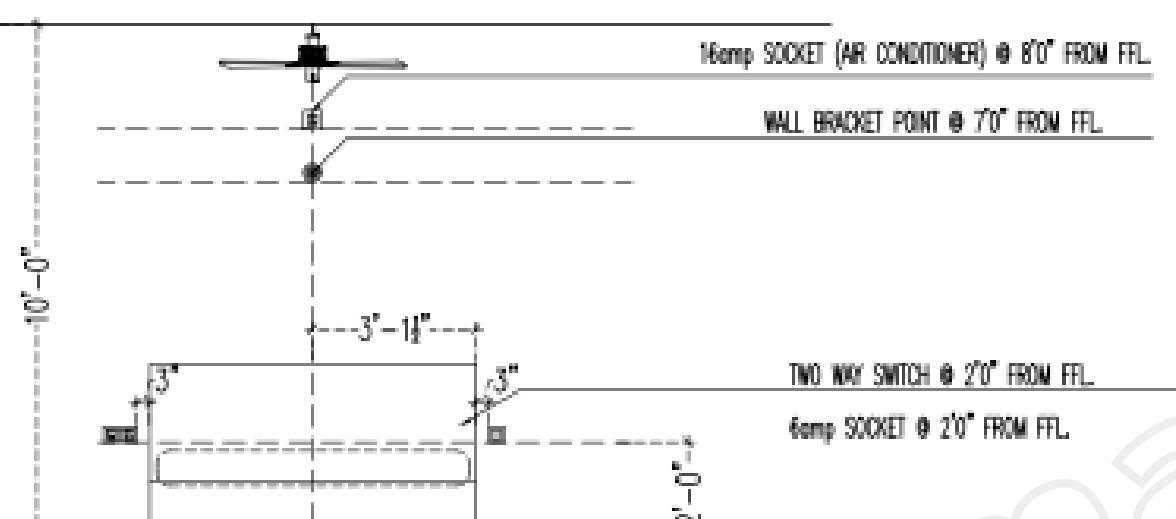

INTERIORS

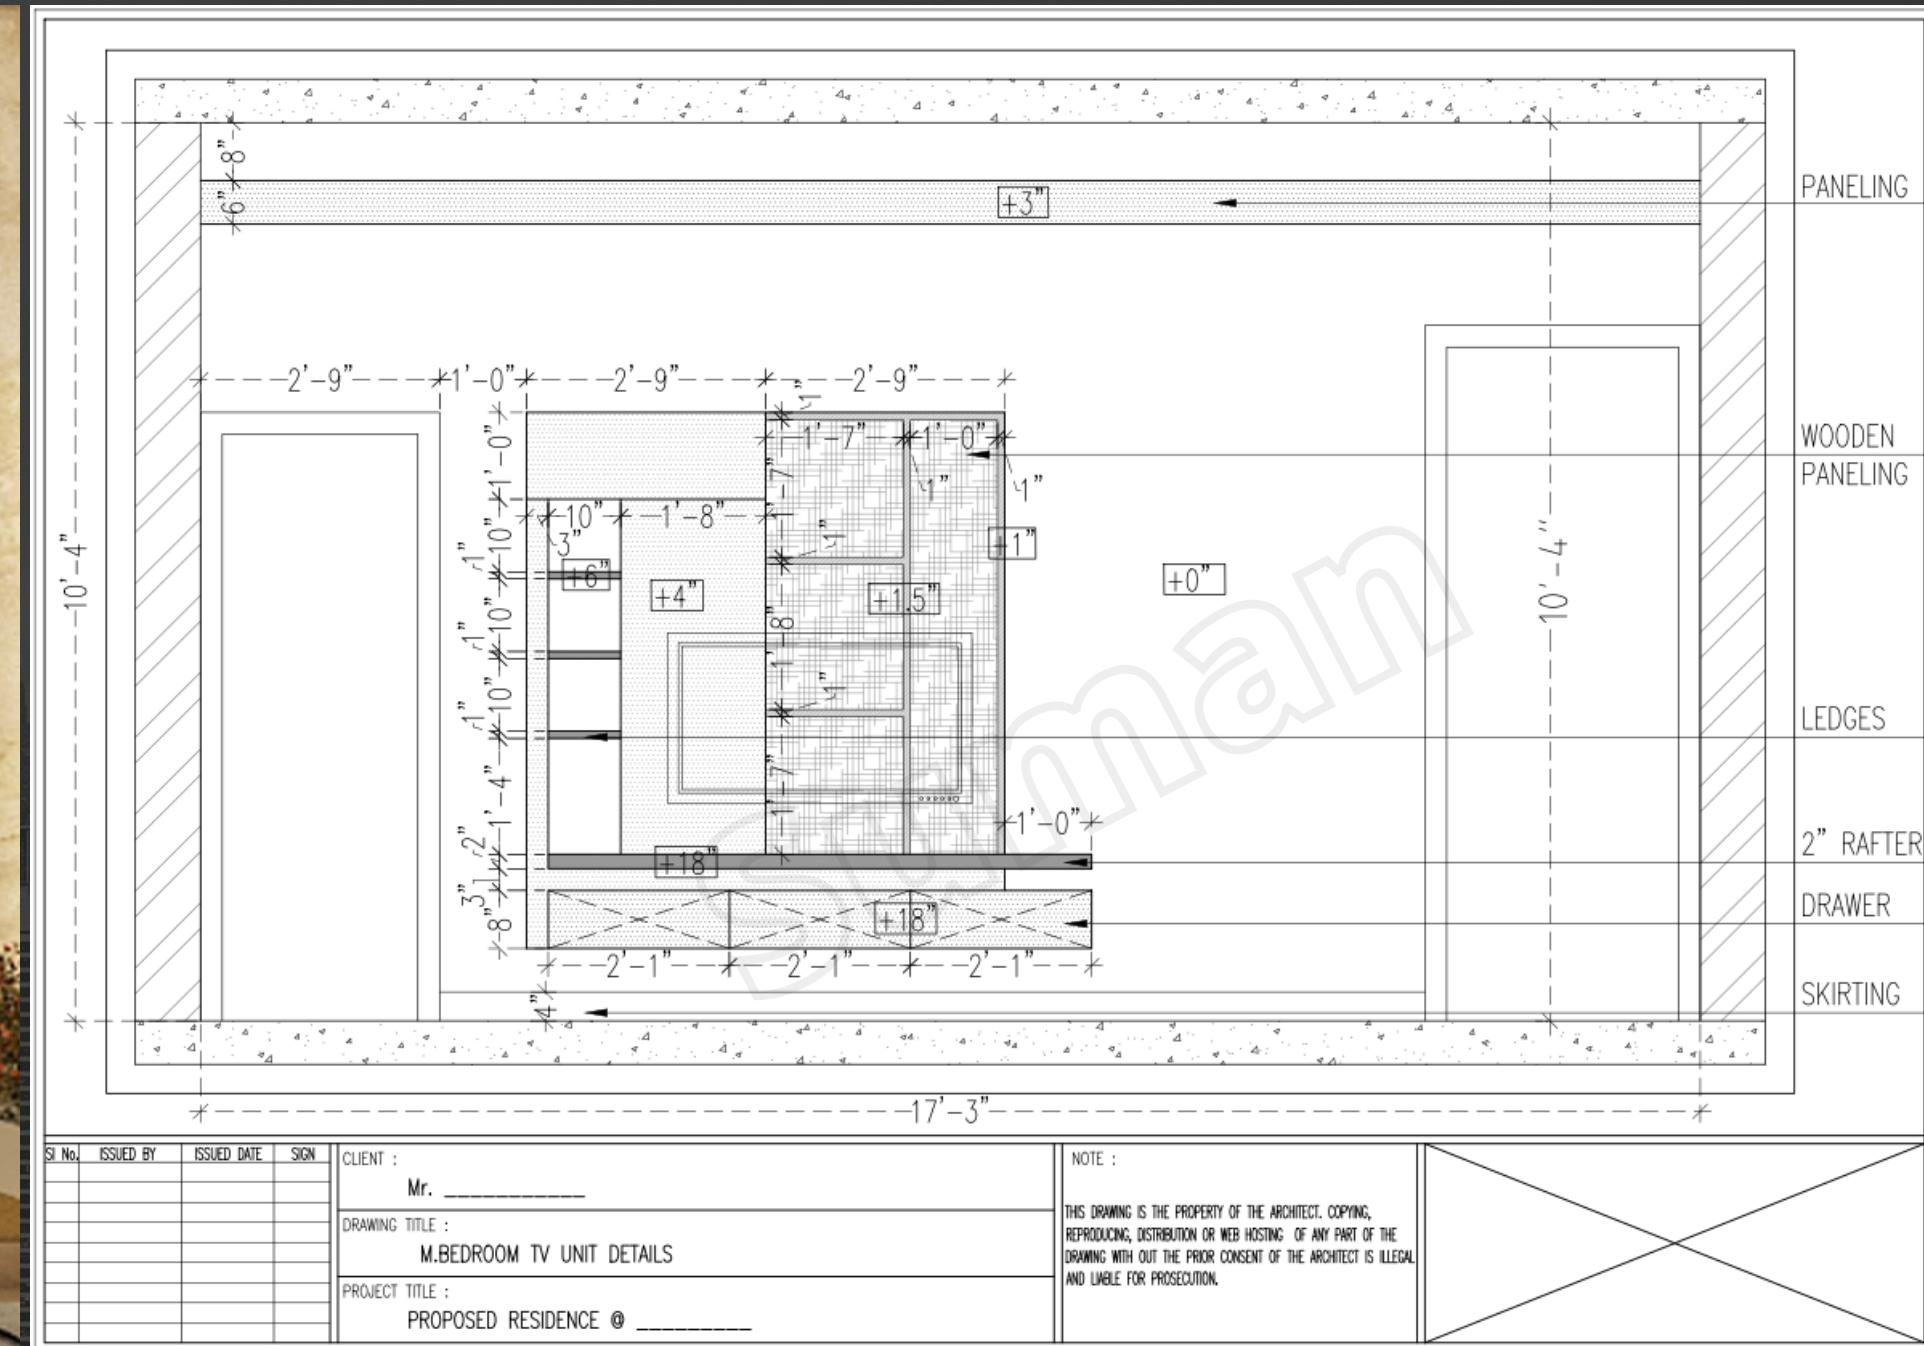

INTERIORS

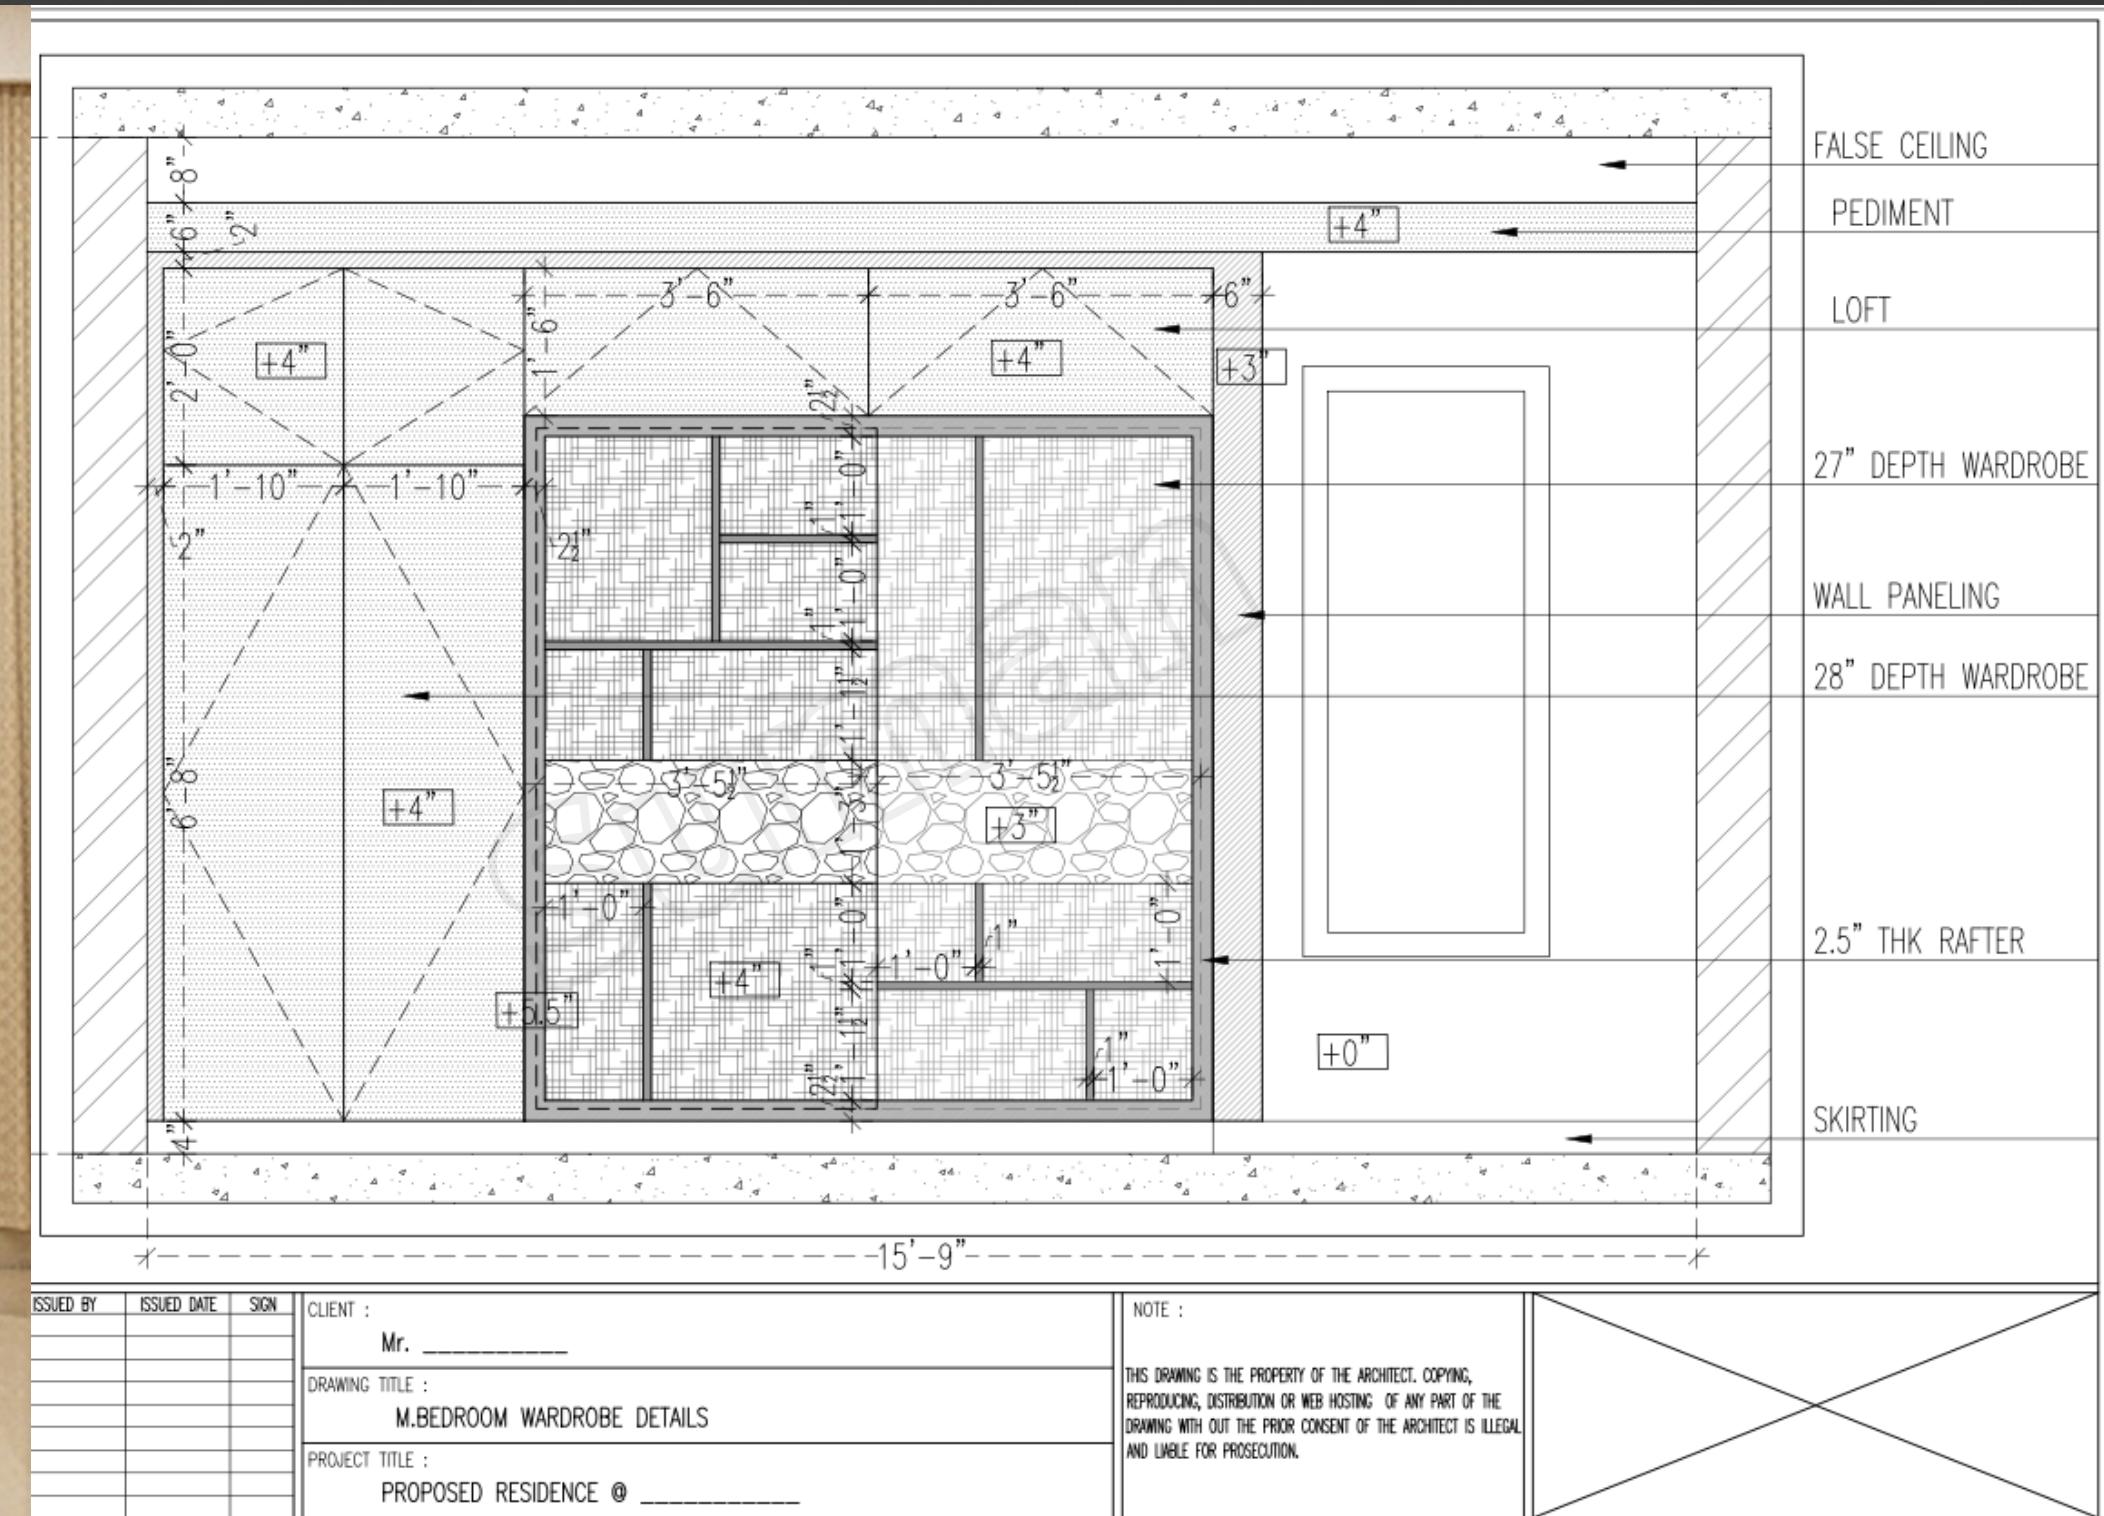

3D ELEVATIONS



3D FLOOR PLANS



3D PRESENTATION





Deals in:

- *Building Constructional Designs & Renovations*
- *2D & 3D Plans*
- *Interior Designs*
- *Estimation & Costing*
- *3D elevation*
- *Approval Plans*